

NODE:24

立體 9F


數量表

圖 例	名 稱	數 量
	綜合消防控制箱	6
	警報逆止閥	2
	差動式探測器	111

圖 例	名 稱	數 量
	定址型監視中繼器 (綜合盤)	6
	定址型監視中繼器 (迴路)	6

警報逆止閥

圖 例	名 稱	數 量
	定址型控制中繼器 (警報狀態)	4
	定址型控制中繼器 (警報狀態)	4

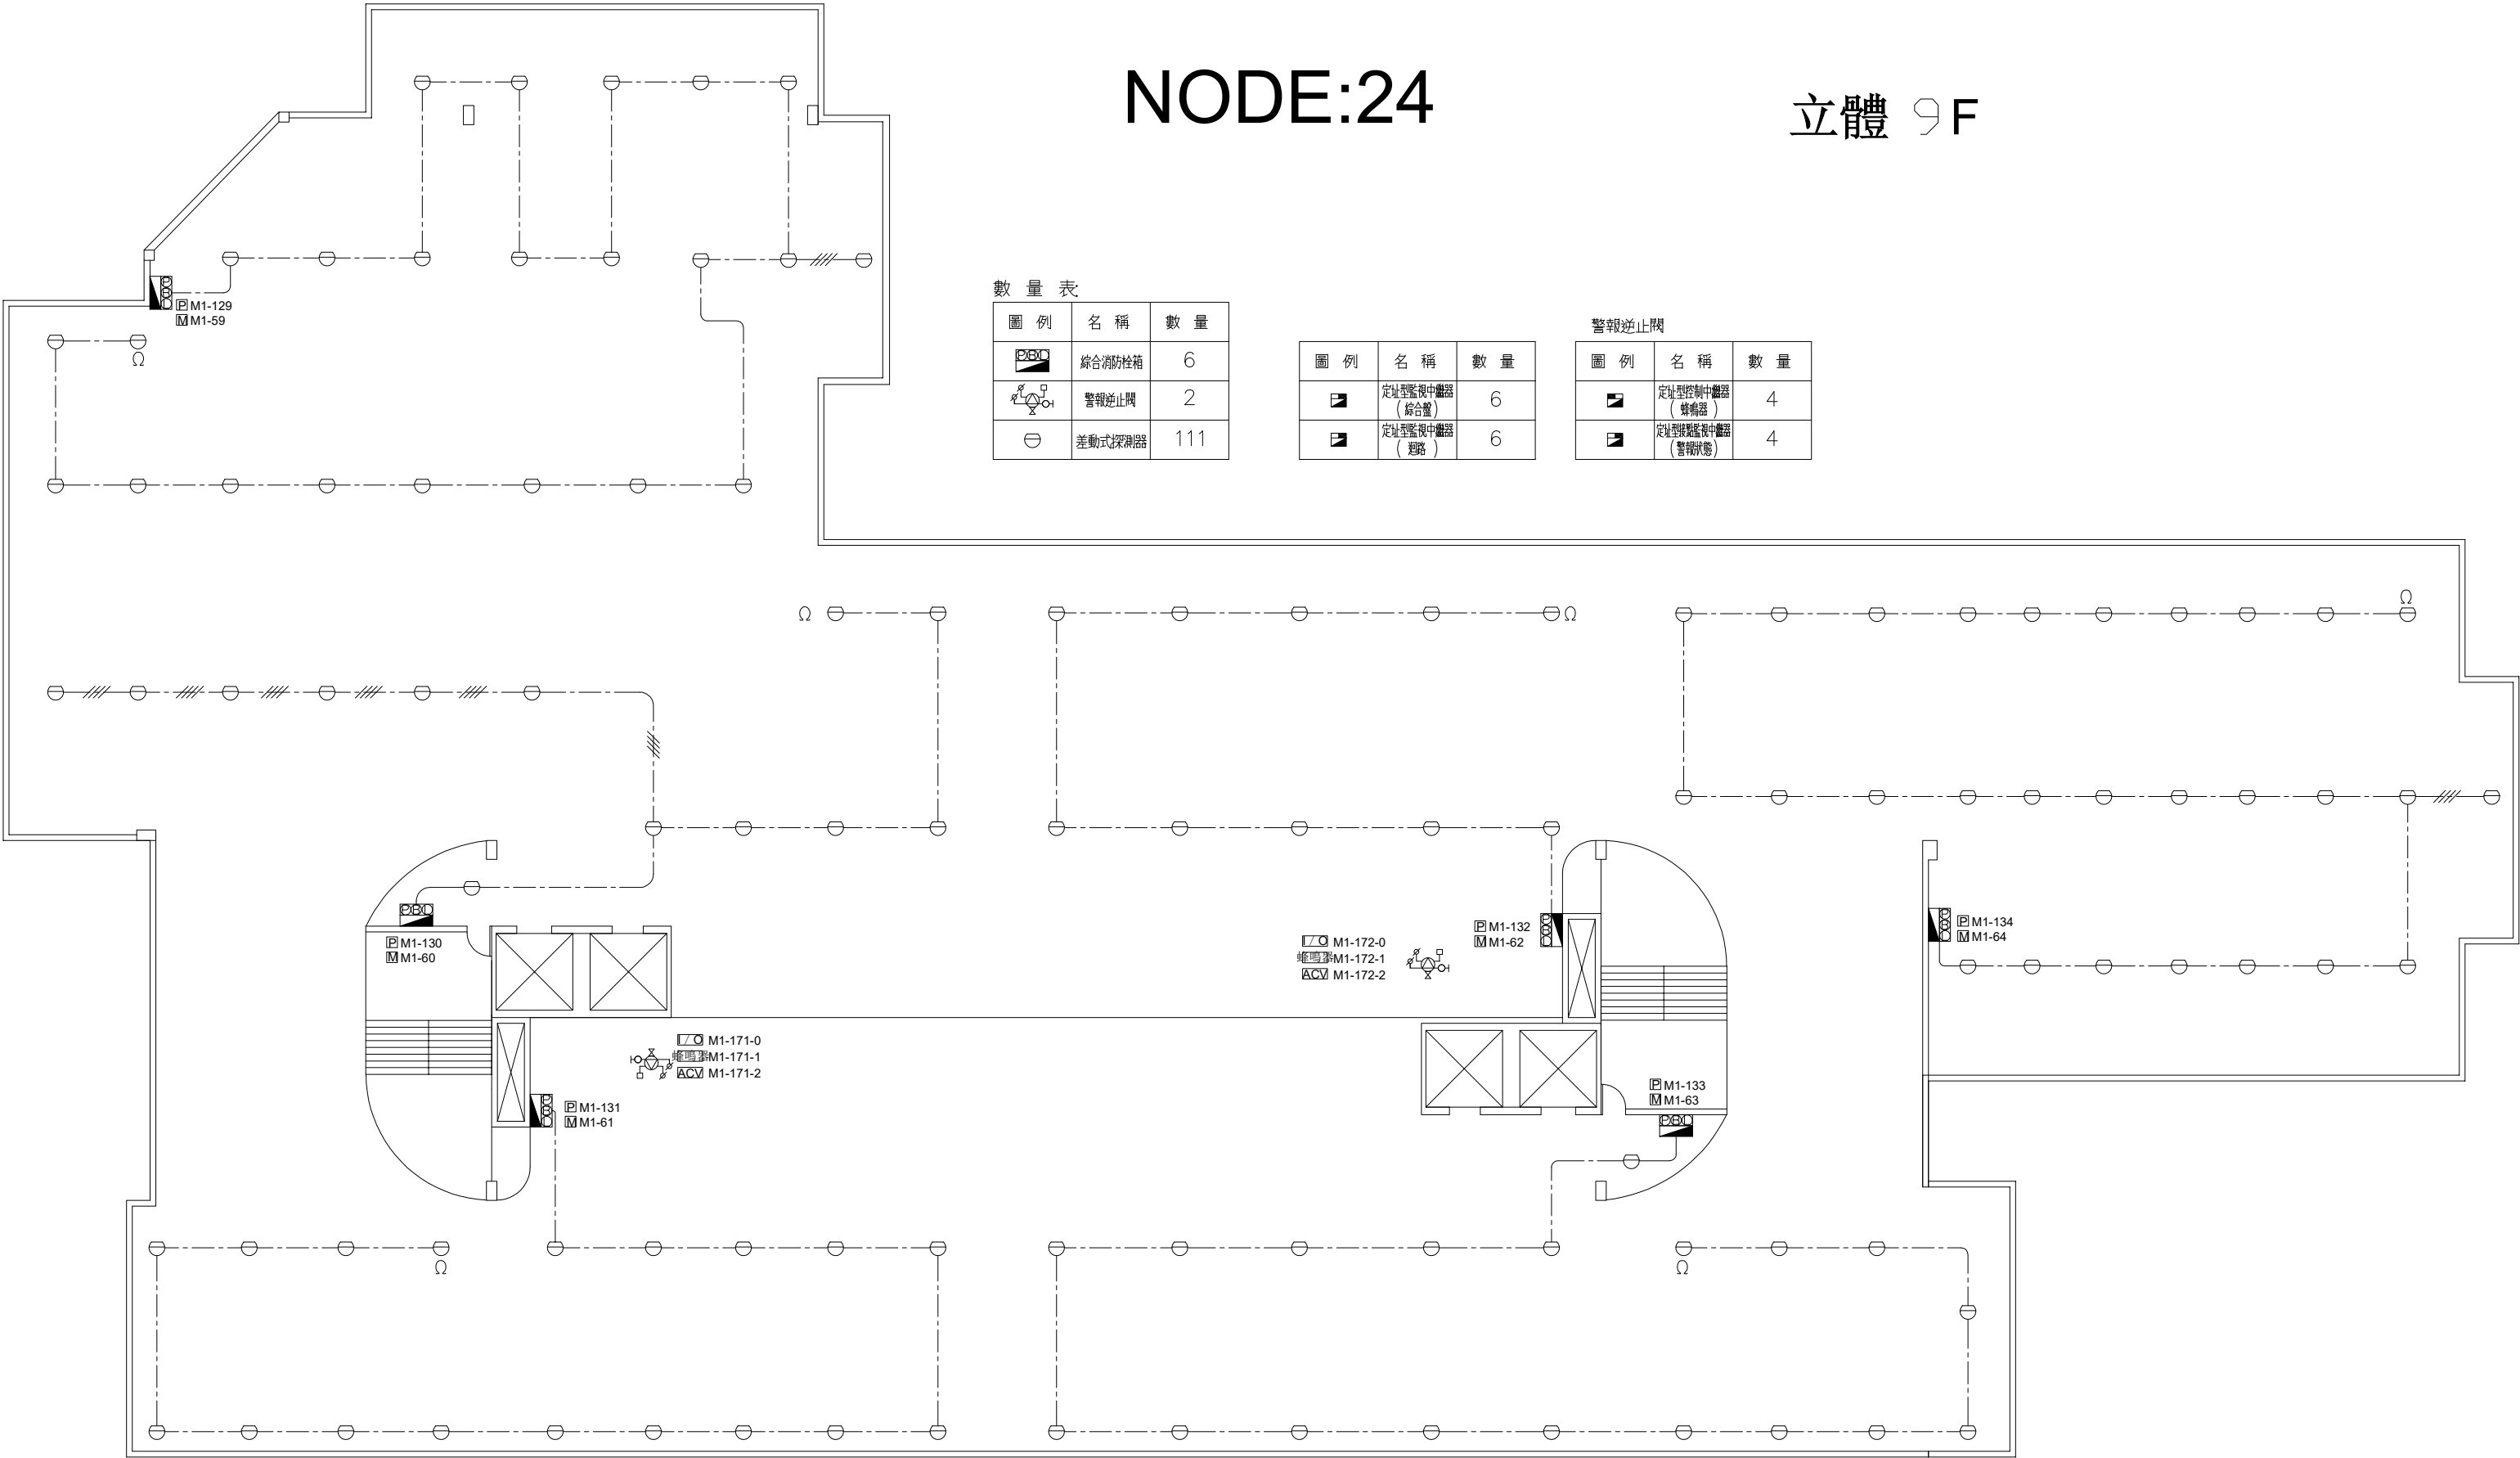

長青科技股?有限公司

電話: (02) 2932-2078(代表) 傳真: (02) 2931-9125

繪圖

設計

校對

修正

REVISION

單位

UNIT

MM

比例

SCALE

日期

DATE

2014.10.16

工程名稱

PROJECT TITLE

本院舊院區火警監視系統財物採購

圖家?容

DRAWING TITLE

台北榮民總醫院 立體停車場
9F消防設備平面圖

工程編號

PROJECT NO

10221070

圖號

DRAWING NO

F-106

張數

SHEET NO