忠源樓 1F

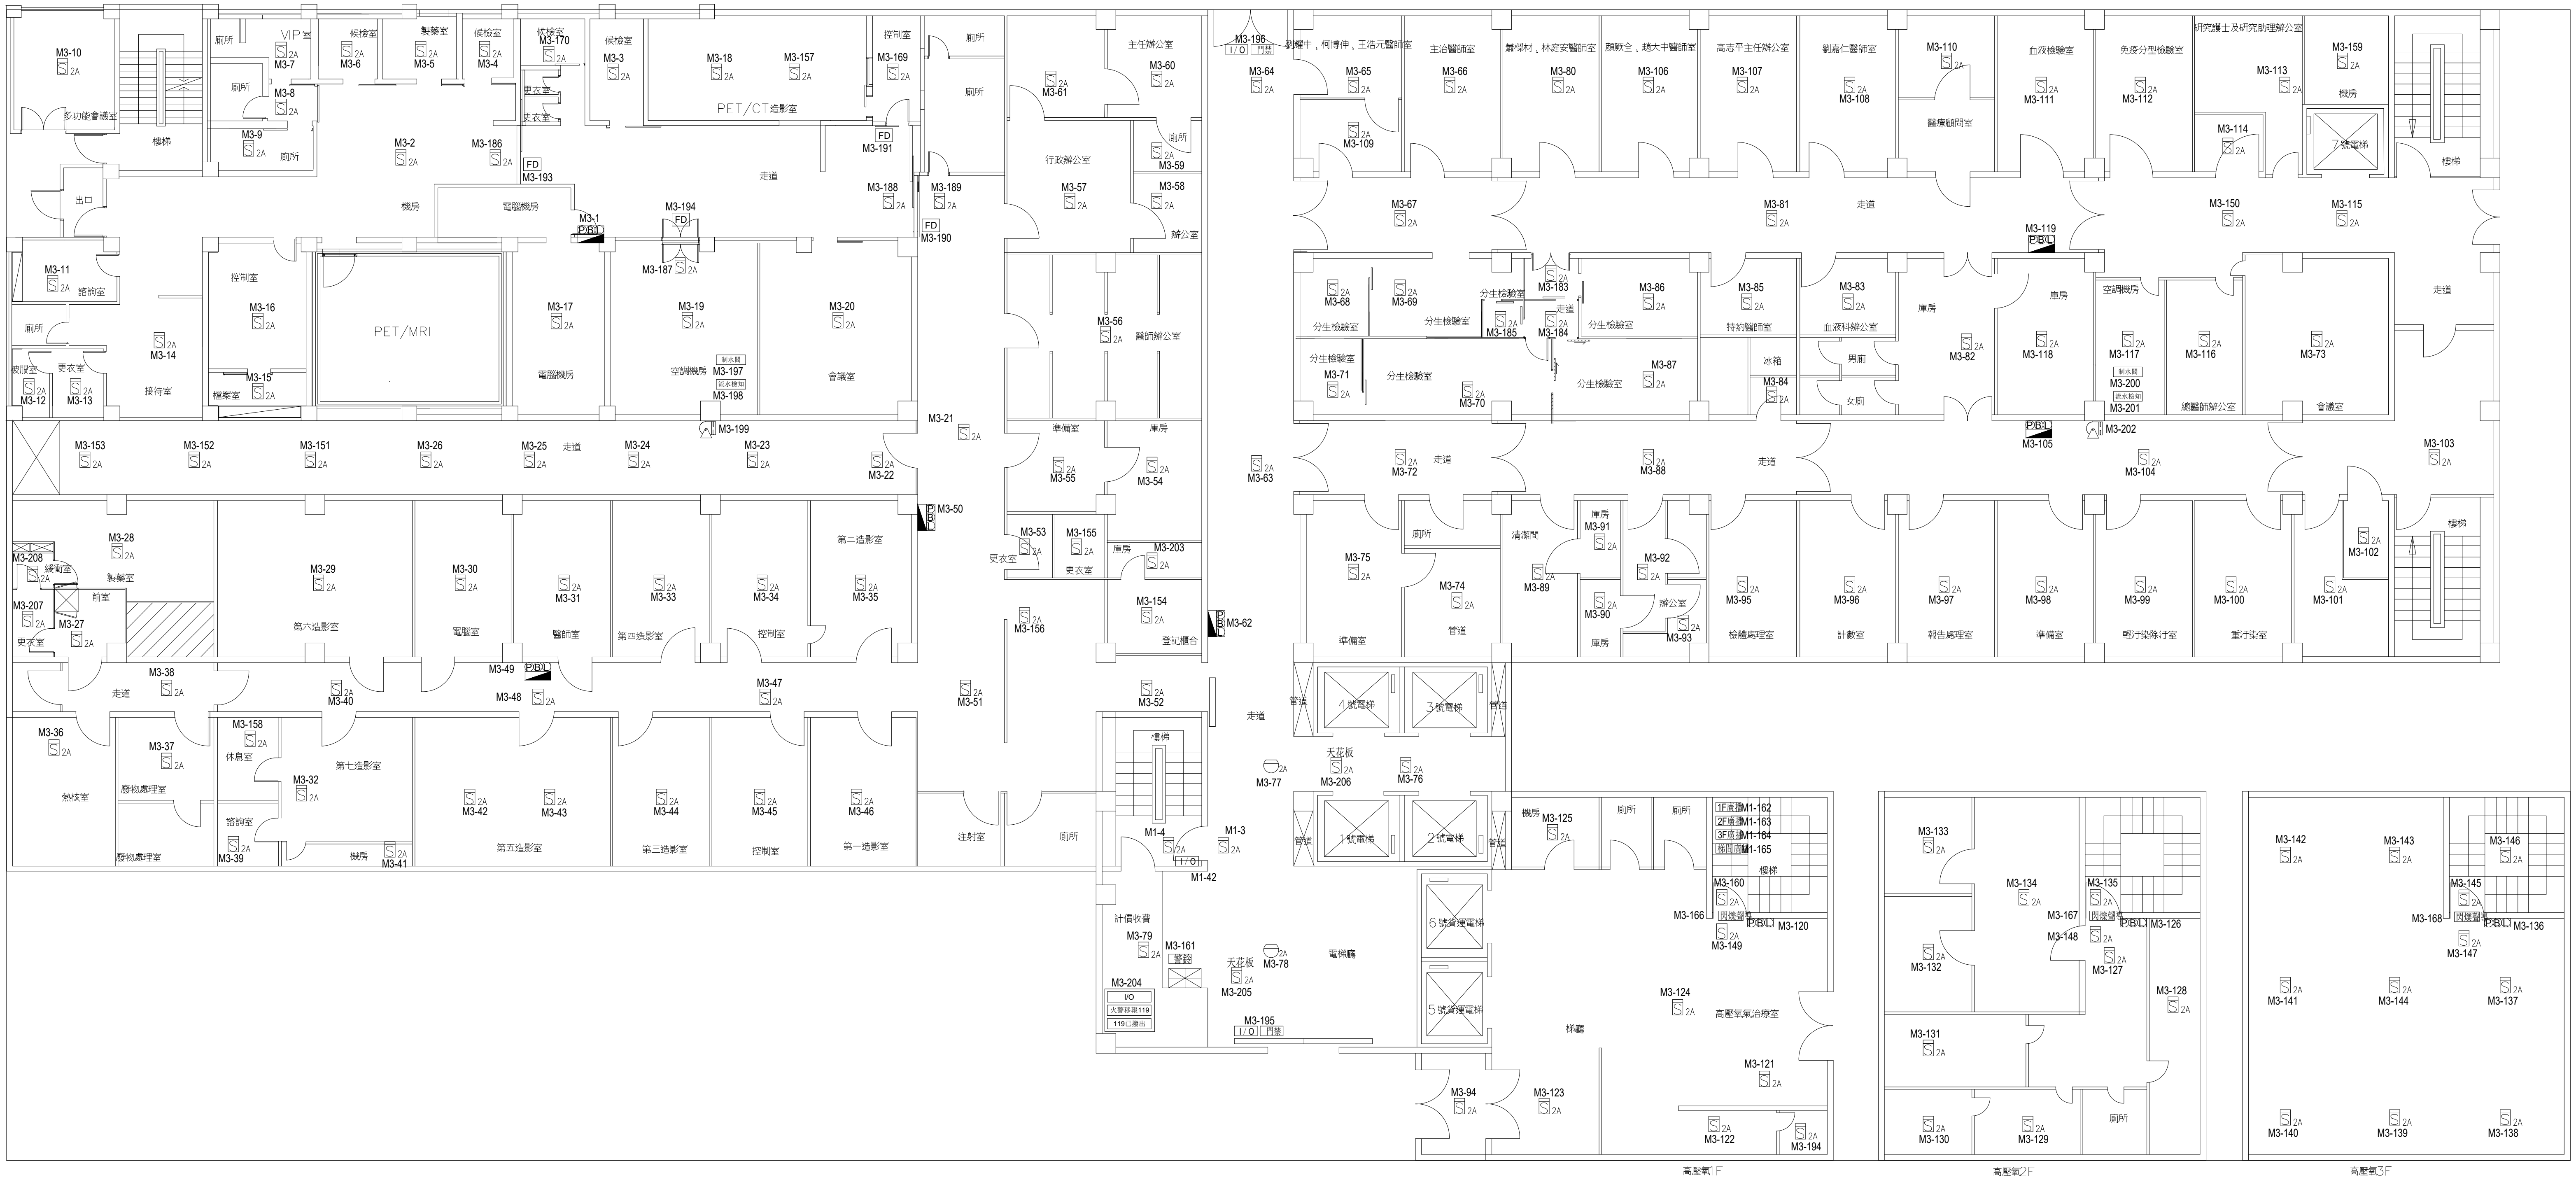
多功能會議室
M3-10
樓梯
VIP室
廁所
M3-7
M3-8
M3-9
候檢室
M3-6
製藥室
M3-5
候檢室
M3-4
候檢室
M3-170
候檢室
M3-3
更衣室
M3-18
M3-157
PET/CT造影室
控制室
M3-169
廁所
廁所
主任辦公室
M3-60
M3-61
M3-196
I/O
門禁
劉耀中，柯博伸，王浩元醫師室
主治醫師室
蕭樑材，林庭安醫師室
顏殿全，趙大中醫師室
高志平主任辦公室
劉嘉仁醫師室
血液檢驗室
免疫分型檢驗室
研究護士及研究助理辦公室
M3-64
M3-65
M3-109
M3-66
M3-80
M3-106
M3-107
M3-108
M3-110
醫療顧問室
M3-111
M3-112
M3-113
M3-159
機房
M3-114
7號電梯
樓梯
出口
M3-2
M3-186
機房
電腦機房
FD
M3-193
M3-1
PBL
M3-194
FD
M3-187
走道
FD
M3-191
M3-188
M3-189
FD
M3-190
行政辦公室
M3-57
廁所
M3-59
M3-58
辦公室
M3-67
M3-81
走道
M3-119
PBL
M3-150
M3-115
走道
M3-11
諮詢室
廁所
被服室
更衣室
M3-12
M3-13
M3-14
接待室
控制室
M3-16
M3-15
檔案室
PET/MRI
M3-17
電腦機房
M3-19
空調機房
制水閥
M3-197
高水隔知
M3-198
M3-20
會議室
M3-56
醫師辦公室
M3-68
分生檢驗室
M3-69
分生檢驗室
M3-183
走道
M3-185
M3-184
分生檢驗室
M3-86
M3-85
特殊醫師室
M3-83
血液科辦公室
庫房
庫房
空調機房
M3-71
分生檢驗室
M3-70
M3-87
分生檢驗室
冰箱
M3-84
男廁
女廁
M3-82
M3-118
M3-117
制水閥
M3-200
高水隔知
M3-201
M3-116
總醫師辦公室
M3-73
會議室
M3-199
M3-21
準備室
庫房
PBL
M3-105
M3-202
M3-153
M3-152
M3-151
M3-26
M3-25
走道
M3-24
M3-23
M3-22
M3-55
M3-54
M3-63
M3-72
走道
M3-88
走道
M3-104
M3-103
M3-28
製藥室
M3-208
緩衝室
前室
M3-207
M3-27
更衣室
M3-29
第六造影室
M3-30
電腦室
M3-31
醫師室
M3-33
第四造影室
M3-34
控制室
第二造影室
M3-35
M3-50
PBL
M3-53
M3-155
更衣室
更衣室
庫房
M3-203
M3-154
登記櫃台
M3-156
M3-62
PBL
M3-75
準備室
廁所
M3-74
管道
清潔間
M3-89
庫房
M3-91
M3-90
庫房
M3-92
辦公室
M3-93
M3-95
檢體處理室
M3-96
計數室
M3-97
報告處理室
M3-98
準備室
M3-99
輕汙染除汙室
M3-100
重汙染室
M3-101
M3-102
樓梯
走道
M3-38
M3-40
M3-49
PBL
M3-48
M3-47
M3-51
M3-52
走道
管道
4號電梯
3號電梯
管道
M3-36
熱核室
M3-37
廢物處理室
廢物處理室
M3-158
休息室
M3-32
第七造影室
諮詢室
M3-39
機房
M3-41
M3-42
M3-43
第五造影室
M3-44
第三造影室
M3-45
控制室
M3-46
第一造影室
注射室
廁所
樓梯
M3-77
天花板
M3-206
M3-76
管道
1號電梯
2號電梯
管道
機房
M3-125
廁所
廁所
1F廣播 M1-162
2F廣播 M1-163
3F廣播 M1-164
排風機 M1-165
樓梯
M1-4
M1-3
I/O
M1-42
計價收費
M3-79
M3-161
警鈴
天花板
M3-205
M3-78
電梯廳
M3-204
I/O
火警移報119
119已撥出
M3-195
I/O
門禁
6號貨運電梯
5號貨運電梯
M3-160
M3-166
閃燈警報
PBL
M3-149
M3-120
M3-124
高壓氧氣治療室
梯廳
M3-121
M3-94
M3-123
M3-122
M3-194
高壓氧1F
M3-133
M3-134
M3-135
M3-167
閃燈警報
PBL
M3-126
M3-148
M3-132
M3-127
M3-128
M3-131
M3-130
M3-129
廁所
高壓氧2F
M3-142
M3-143
M3-146
M3-145
M3-168
閃燈警報
PBL
M3-136
M3-147
M3-141
M3-144
M3-137
M3-140
M3-139
M3-138
高壓氧3F