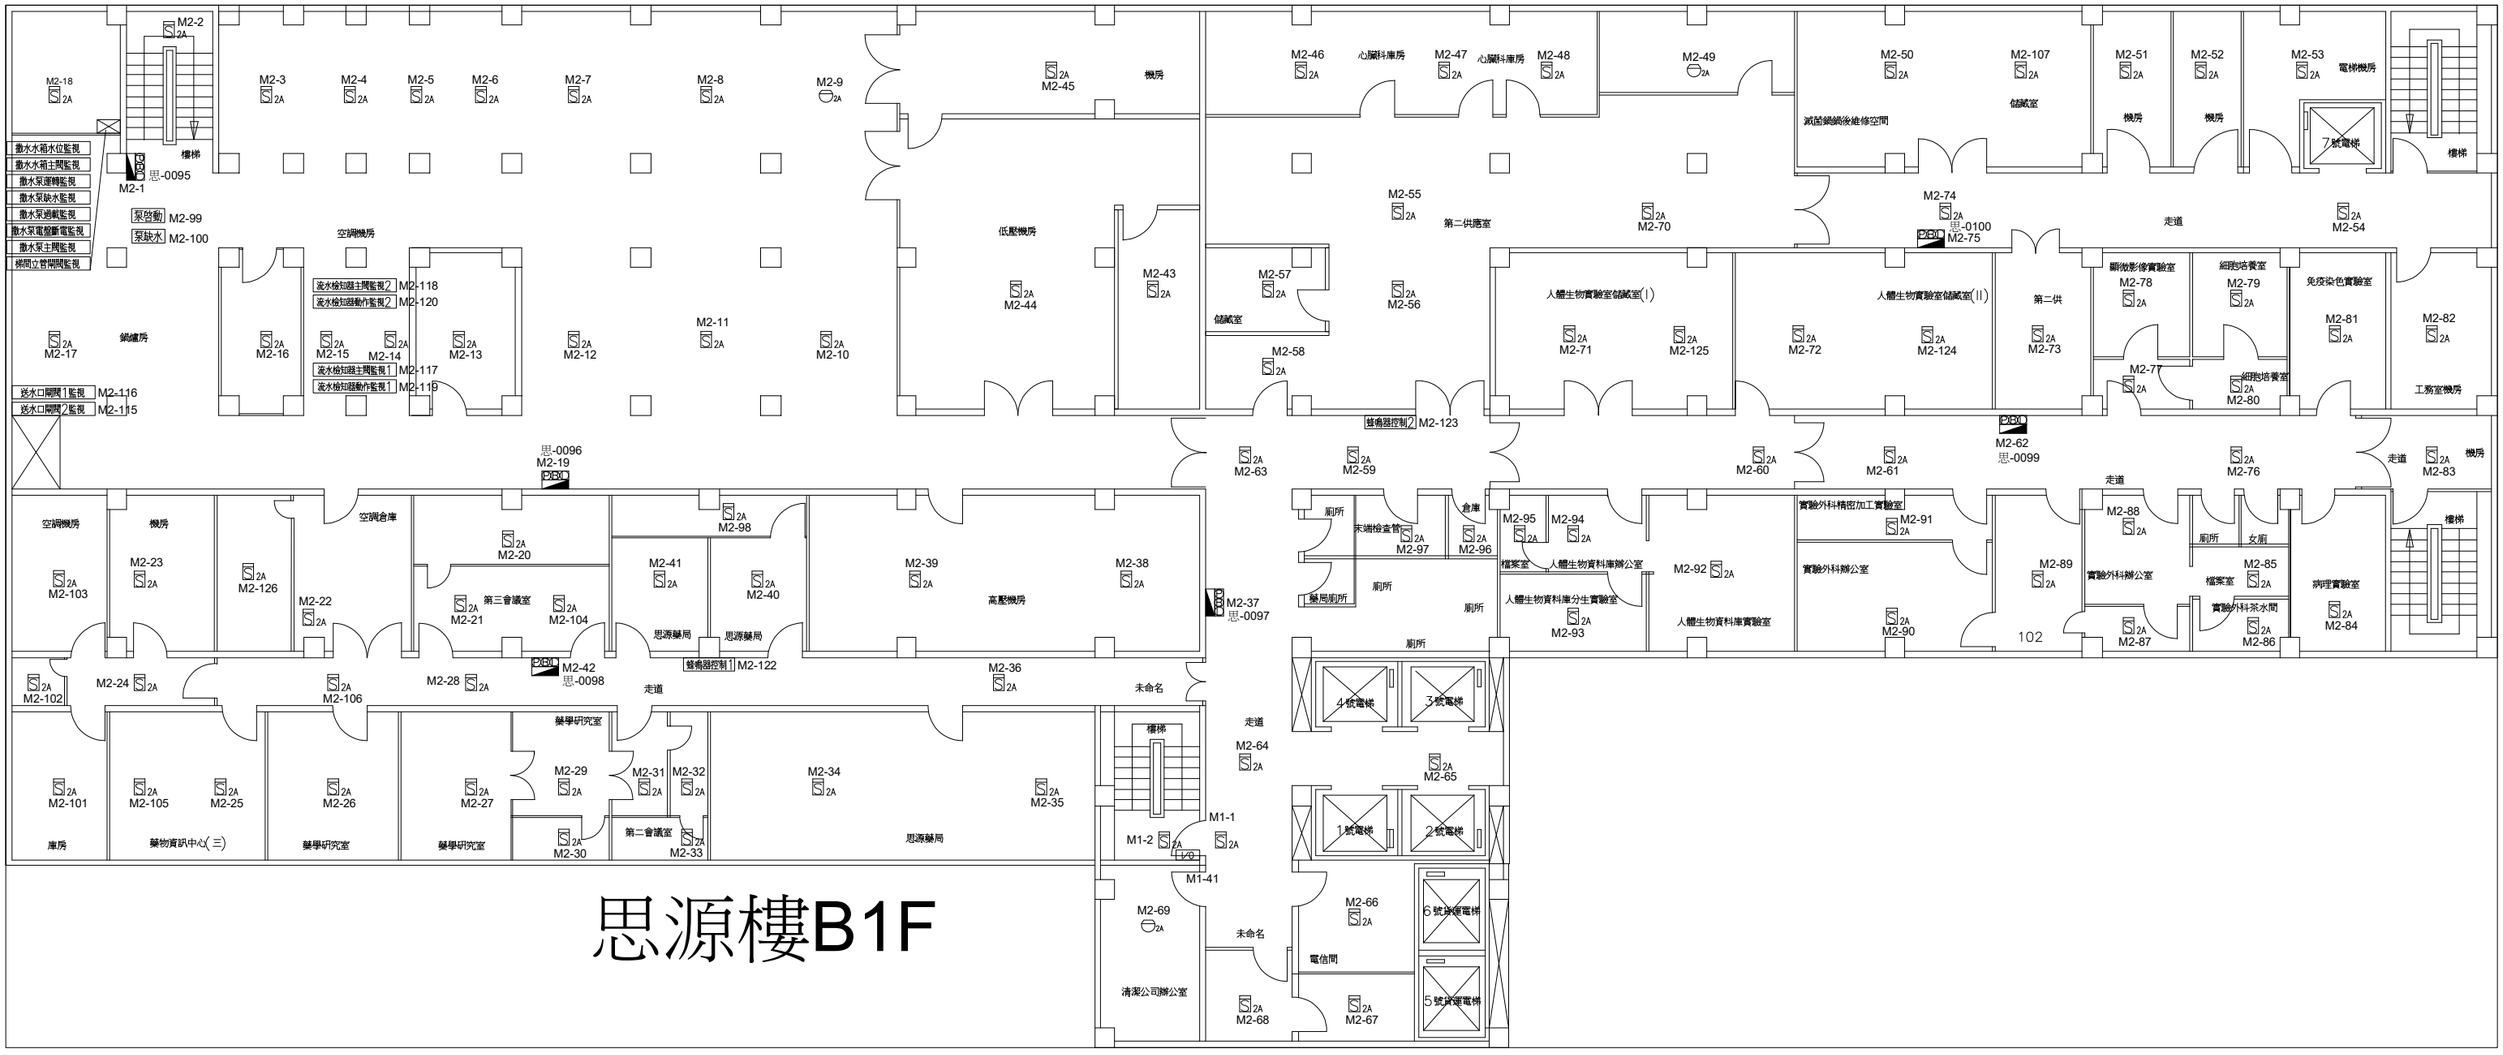
M2-108 散水箱水位監視
M2-109 散水水箱主閥監視
M2-110 散水泵運轉監視
M2-111 散水泵缺水監視
M2-112 散水泵過載監視
M2-113 散水泵電壓斷電監視
M2-114 散水泵主閥監視
M2-121 機閥立管開閥監視
泵啓動 M2-99
泵缺水 M2-100
送水檢知器主閥監視2 M2-118
送水檢知器動作監視2 M2-120
送水檢知器主閥監視1 M2-117
送水檢知器動作監視1 M2-119
送水口開閥1監視 M2-116
送水口開閥2監視 M2-115
鍋爐房
空調機房
空調倉庫
第三會議室
思源藥局
低壓機房
高壓機房
第二供應室
減菌鍋鍋後維修空間
儲藏室
人體生物實驗室儲藏室(I)
人體生物實驗室儲藏室(II)
第二供
顯微影像實驗室
細胞培養室
免疫染色實驗室
工務室機房
電梯機房
1號電梯
2號電梯
3號電梯
4號電梯
5號貨運電梯
6號貨運電梯
檔案室
人體生物資料庫辦公室
人體生物資料庫分生實驗室
人體生物資料庫實驗室
實驗外科精密加工實驗室
實驗外科辦公室
實驗外科茶水間
病理實驗室
藥學研究室
藥物資訊中心(三)
第二會議室
未命名
清潔公司辦公室
電信間
倉庫
廁所
女廁
走道
102
思-0095
思-0096
思-0097
思-0098
思-0099
思-0100
M2-1
M2-2
M2-3
M2-4
M2-5
M2-6
M2-7
M2-8
M2-9
M2-10
M2-11
M2-12
M2-13
M2-14
M2-15
M2-16
M2-17
M2-18
M2-19
M2-20
M2-21
M2-22
M2-23
M2-24
M2-25
M2-26
M2-27
M2-28
M2-29
M2-30
M2-31
M2-32
M2-33
M2-34
M2-35
M2-36
M2-37
M2-38
M2-39
M2-40
M2-41
M2-42
M2-43
M2-44
M2-45
M2-46
M2-47
M2-48
M2-49
M2-50
M2-51
M2-52
M2-53
M2-54
M2-55
M2-56
M2-57
M2-58
M2-59
M2-60
M2-61
M2-62
M2-63
M2-64
M2-65
M2-66
M2-67
M2-68
M2-69
M2-70
M2-71
M2-72
M2-73
M2-74
M2-75
M2-76
M2-77
M2-78
M2-79
M2-80
M2-81
M2-82
M2-83
M2-84
M2-85
M2-86
M2-87
M2-88
M2-89
M2-90
M2-91
M2-92
M2-93
M2-94
M2-95
M2-96
M2-97
M2-98
M2-101
M2-102
M2-103
M2-104
M2-105
M2-106
M2-107
M2-122
M2-123
M2-124
M2-125
M2-126
M1-1
M1-2
M1-41
機房
儲藏室
檔梯
走道
未命名
廁所
倉庫
電梯機房
2A
EXIT
思源藥局
高壓機房
空調倉庫
空調機房
機房
藥學研究室
藥物資訊中心(三)
庫房
第三會議室
第二會議室
鍋爐房
儲藏室
檔梯
走道
未命名
廁所
倉庫
電梯機房
1號電梯
2號電梯
3號電梯
4號電梯
5號貨運電梯
6號貨運電梯
檔案室
人體生物資料庫辦公室
人體生物資料庫分生實驗室
人體生物資料庫實驗室
實驗外科精密加工實驗室
實驗外科辦公室
實驗外科茶水間
病理實驗室
顯微影像實驗室
細胞培養室
免疫染色實驗室
工務室機房
第二供
人體生物實驗室儲藏室(I)
人體生物實驗室儲藏室(II)
減菌鍋鍋後維修空間
電信間
清潔公司辦公室
思源藥局
思源藥局
藥局廁所
廁所
女廁
走道
102
思-0095
思-0096
思-0097
思-0098
思-0099
思-0100

思源樓B1F