


NODE:21
技警1F

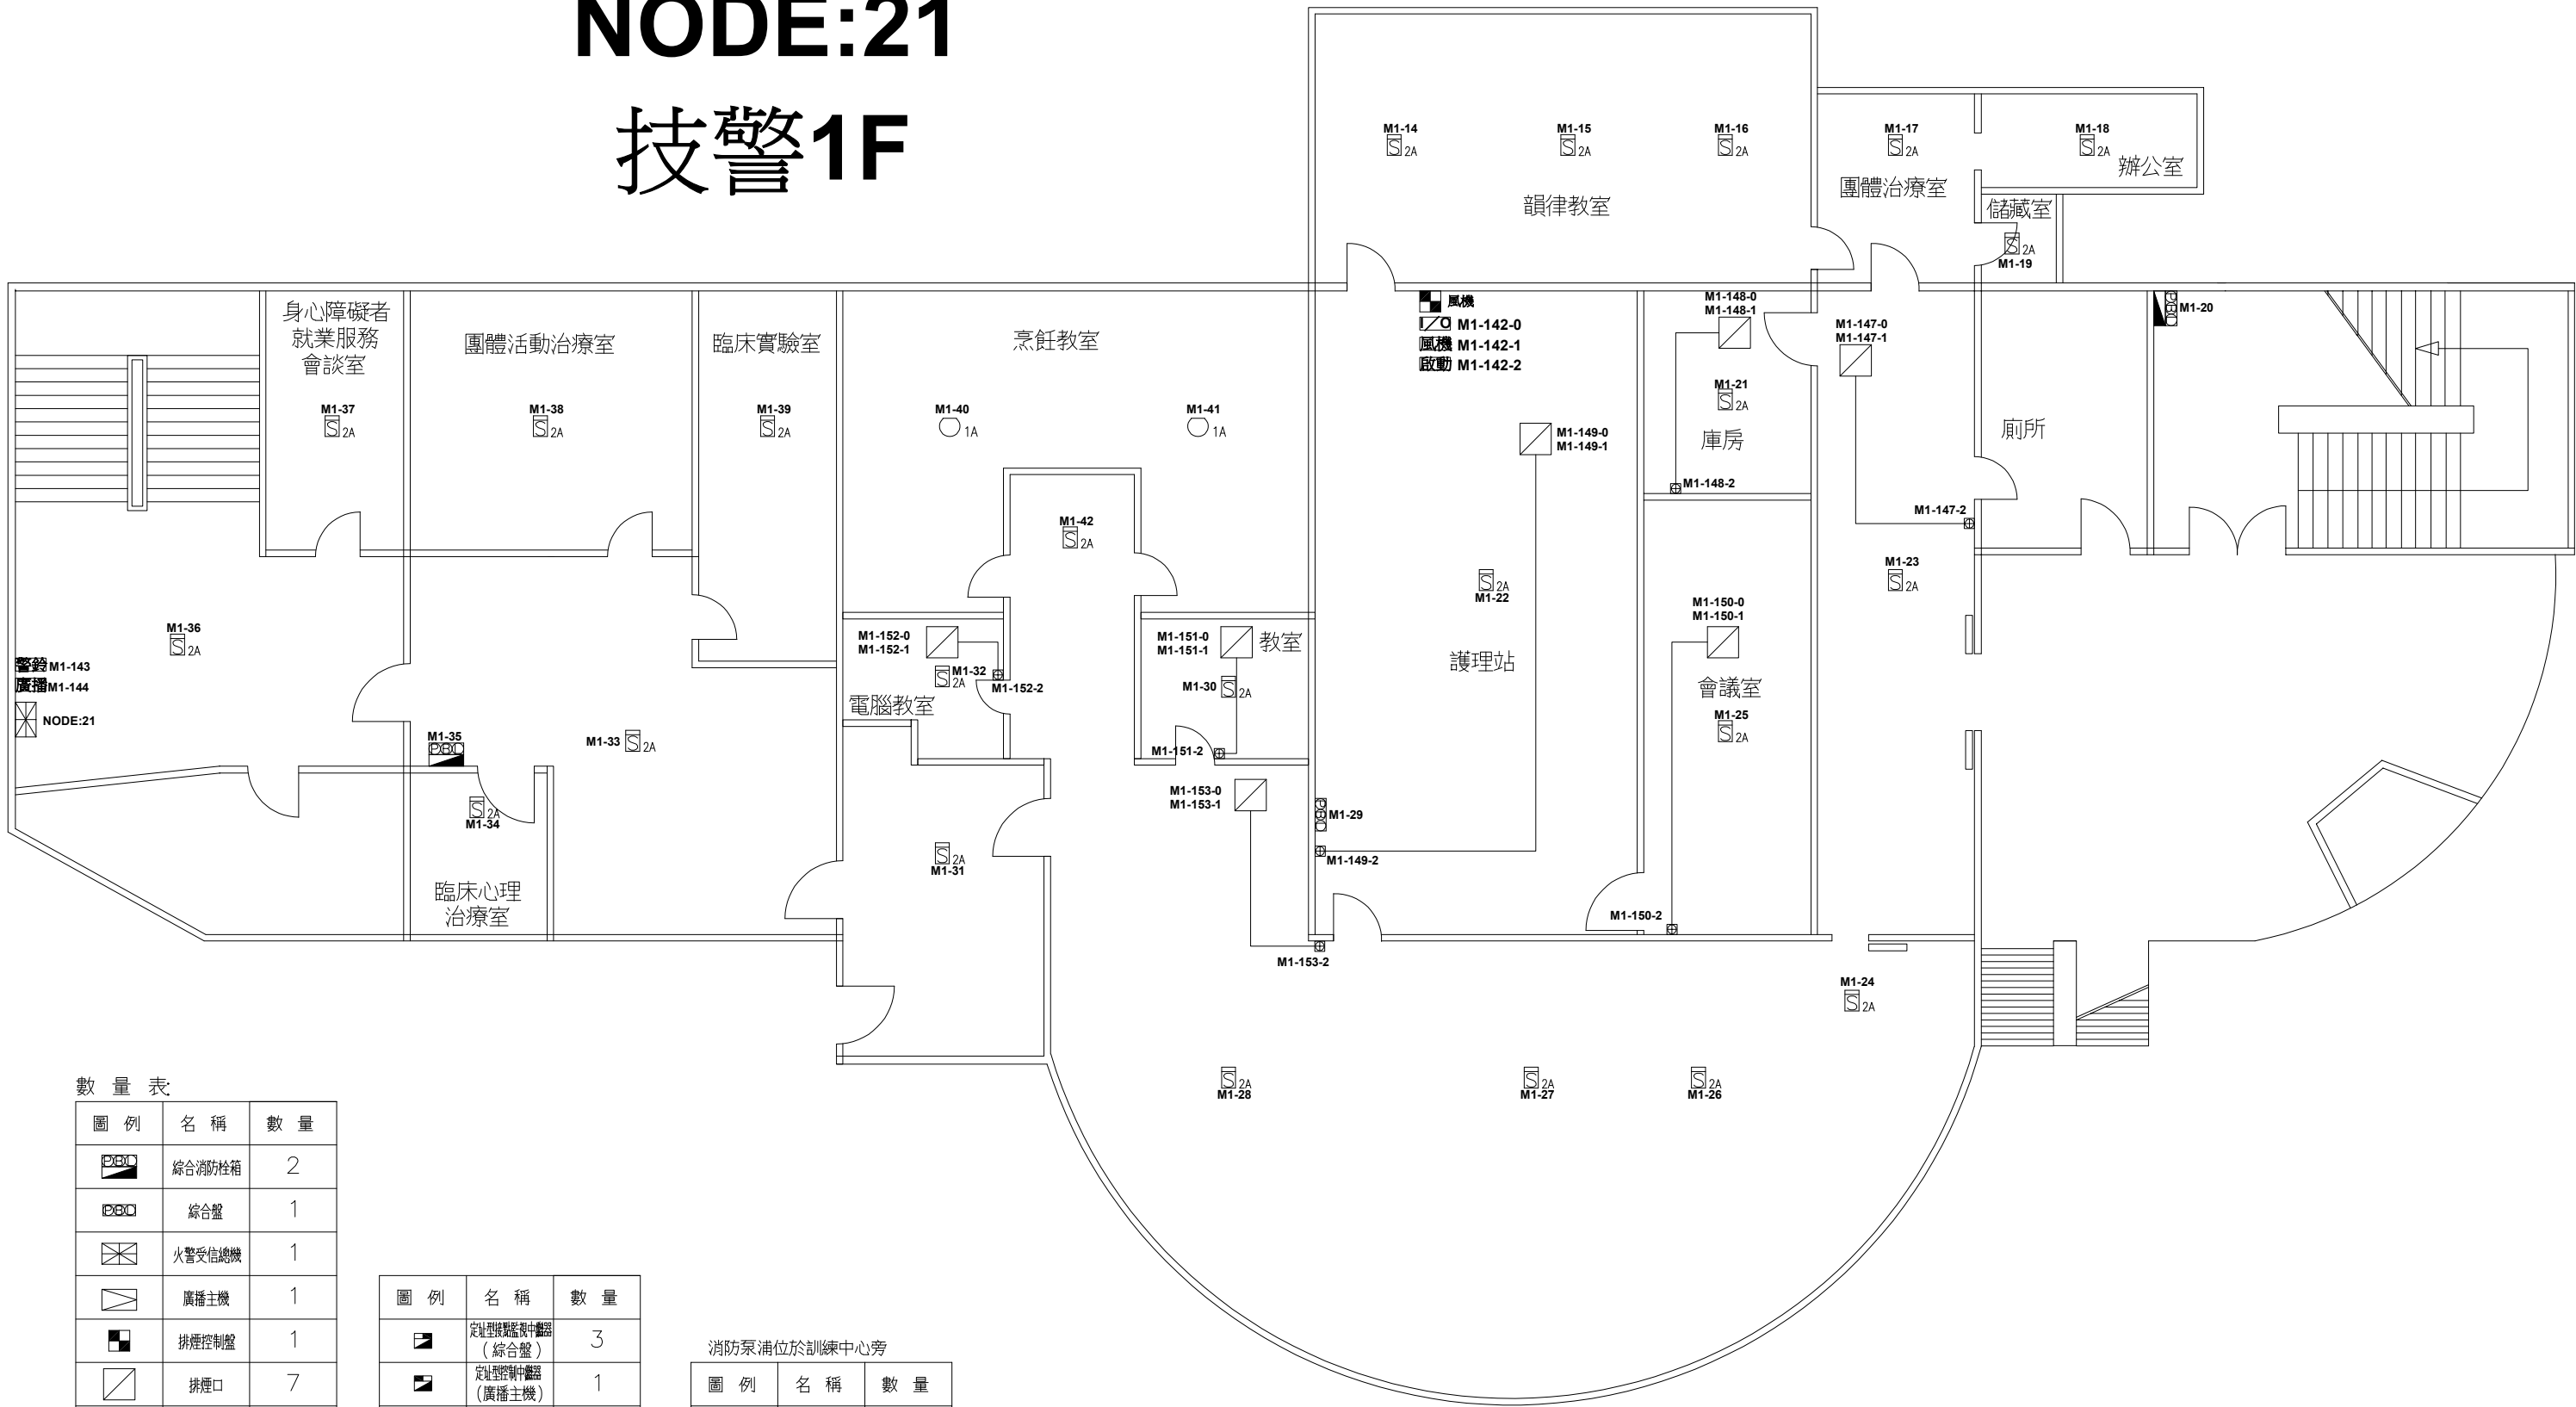

數量表

圖 例	名 稱	數 量
	綜合消防栓箱	2
	綜合盤	1
	火警受信總機	1
	廣播主機	1
	排煙控制盤	1
	排煙口	7
	偵煙探測器 (定址式)	24
	定溫探測器 (定址式)	2

圖 例	名 稱	數 量
	定址型控制盤中繼器 (綜合盤)	3
	定址型控制盤中繼器 (廣播主機)	1
	定址型控制盤中繼器 (排煙控制盤)	1
	定址型控制盤中繼器 (排煙口)	7

消防泵浦位於訓練中心旁

圖 例	名 稱	數 量
	定址型控制中繼器 (泵啟動)	1
	定址型監視中繼器 (泵缺水狀態)	1