


NODE:21

技警B1F

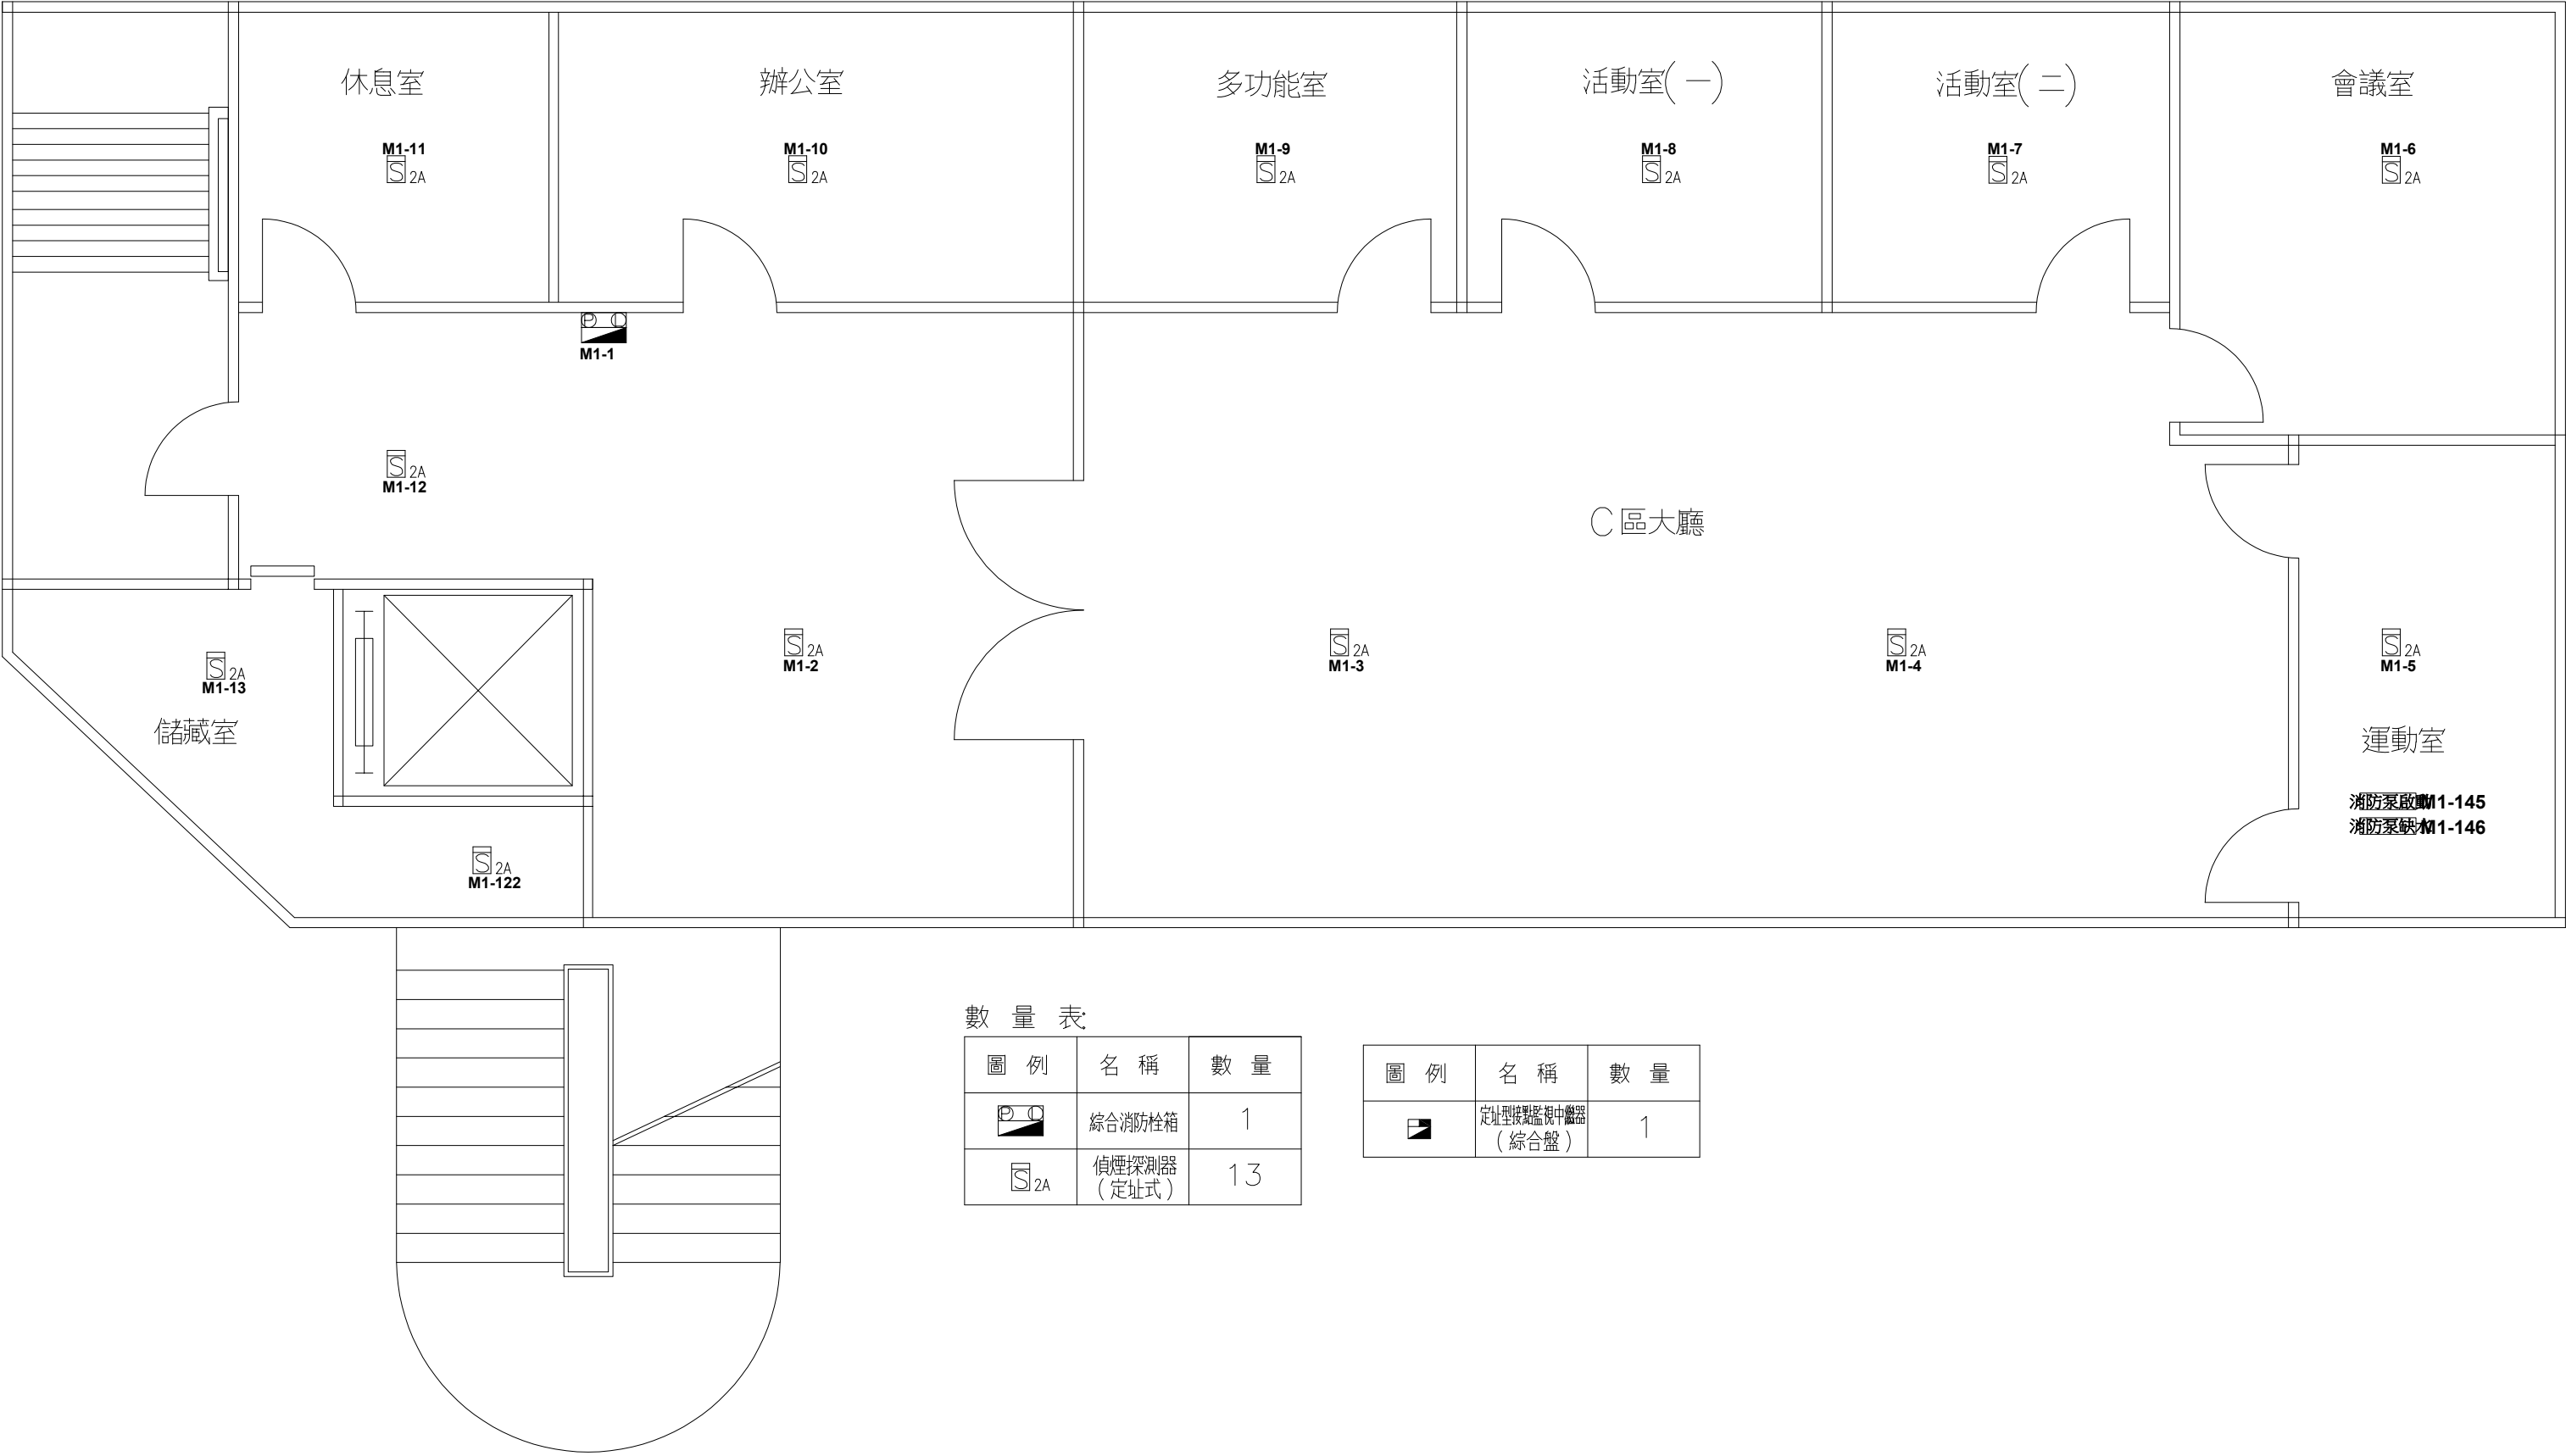

數 量 表

圖 例	名 稱	數 量
	綜合消防栓箱	1
	偵煙探測器 (定址式)	13

圖 例	名 稱	數 量
	定址型接點監視中繼器 (綜合盤)	1