


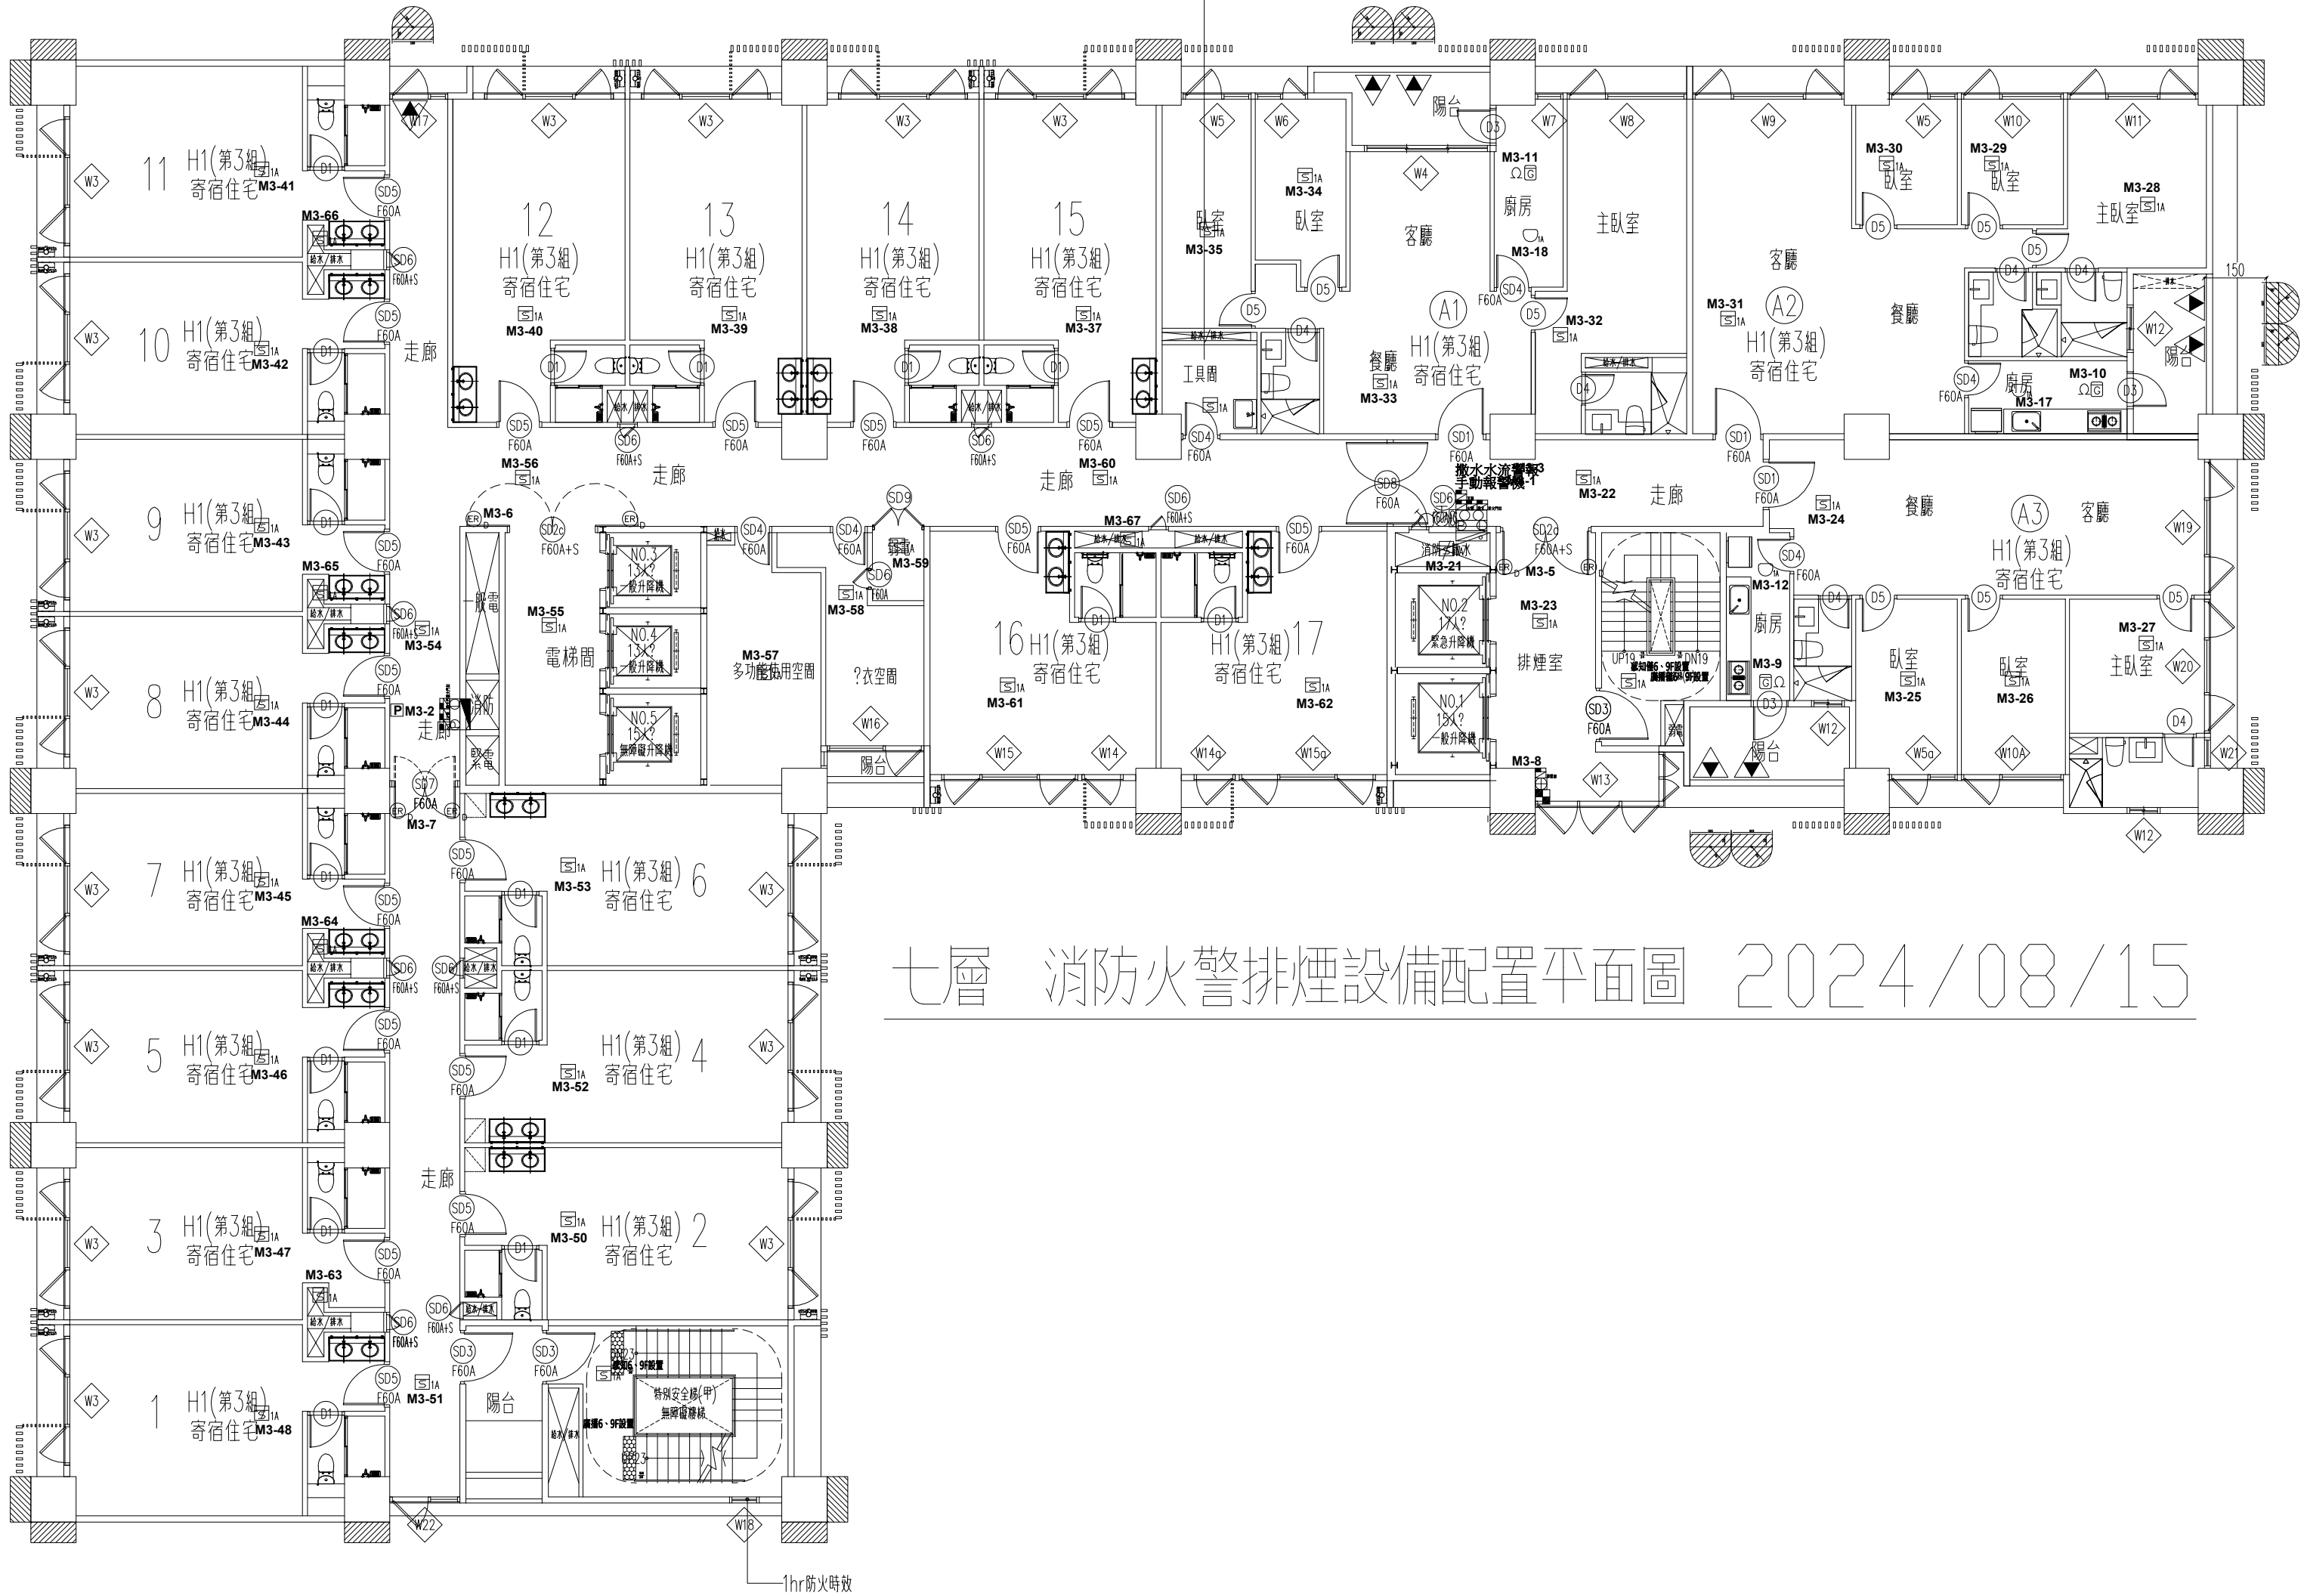

七層 消防火警排煙設備配置平面圖 2024/08/15