


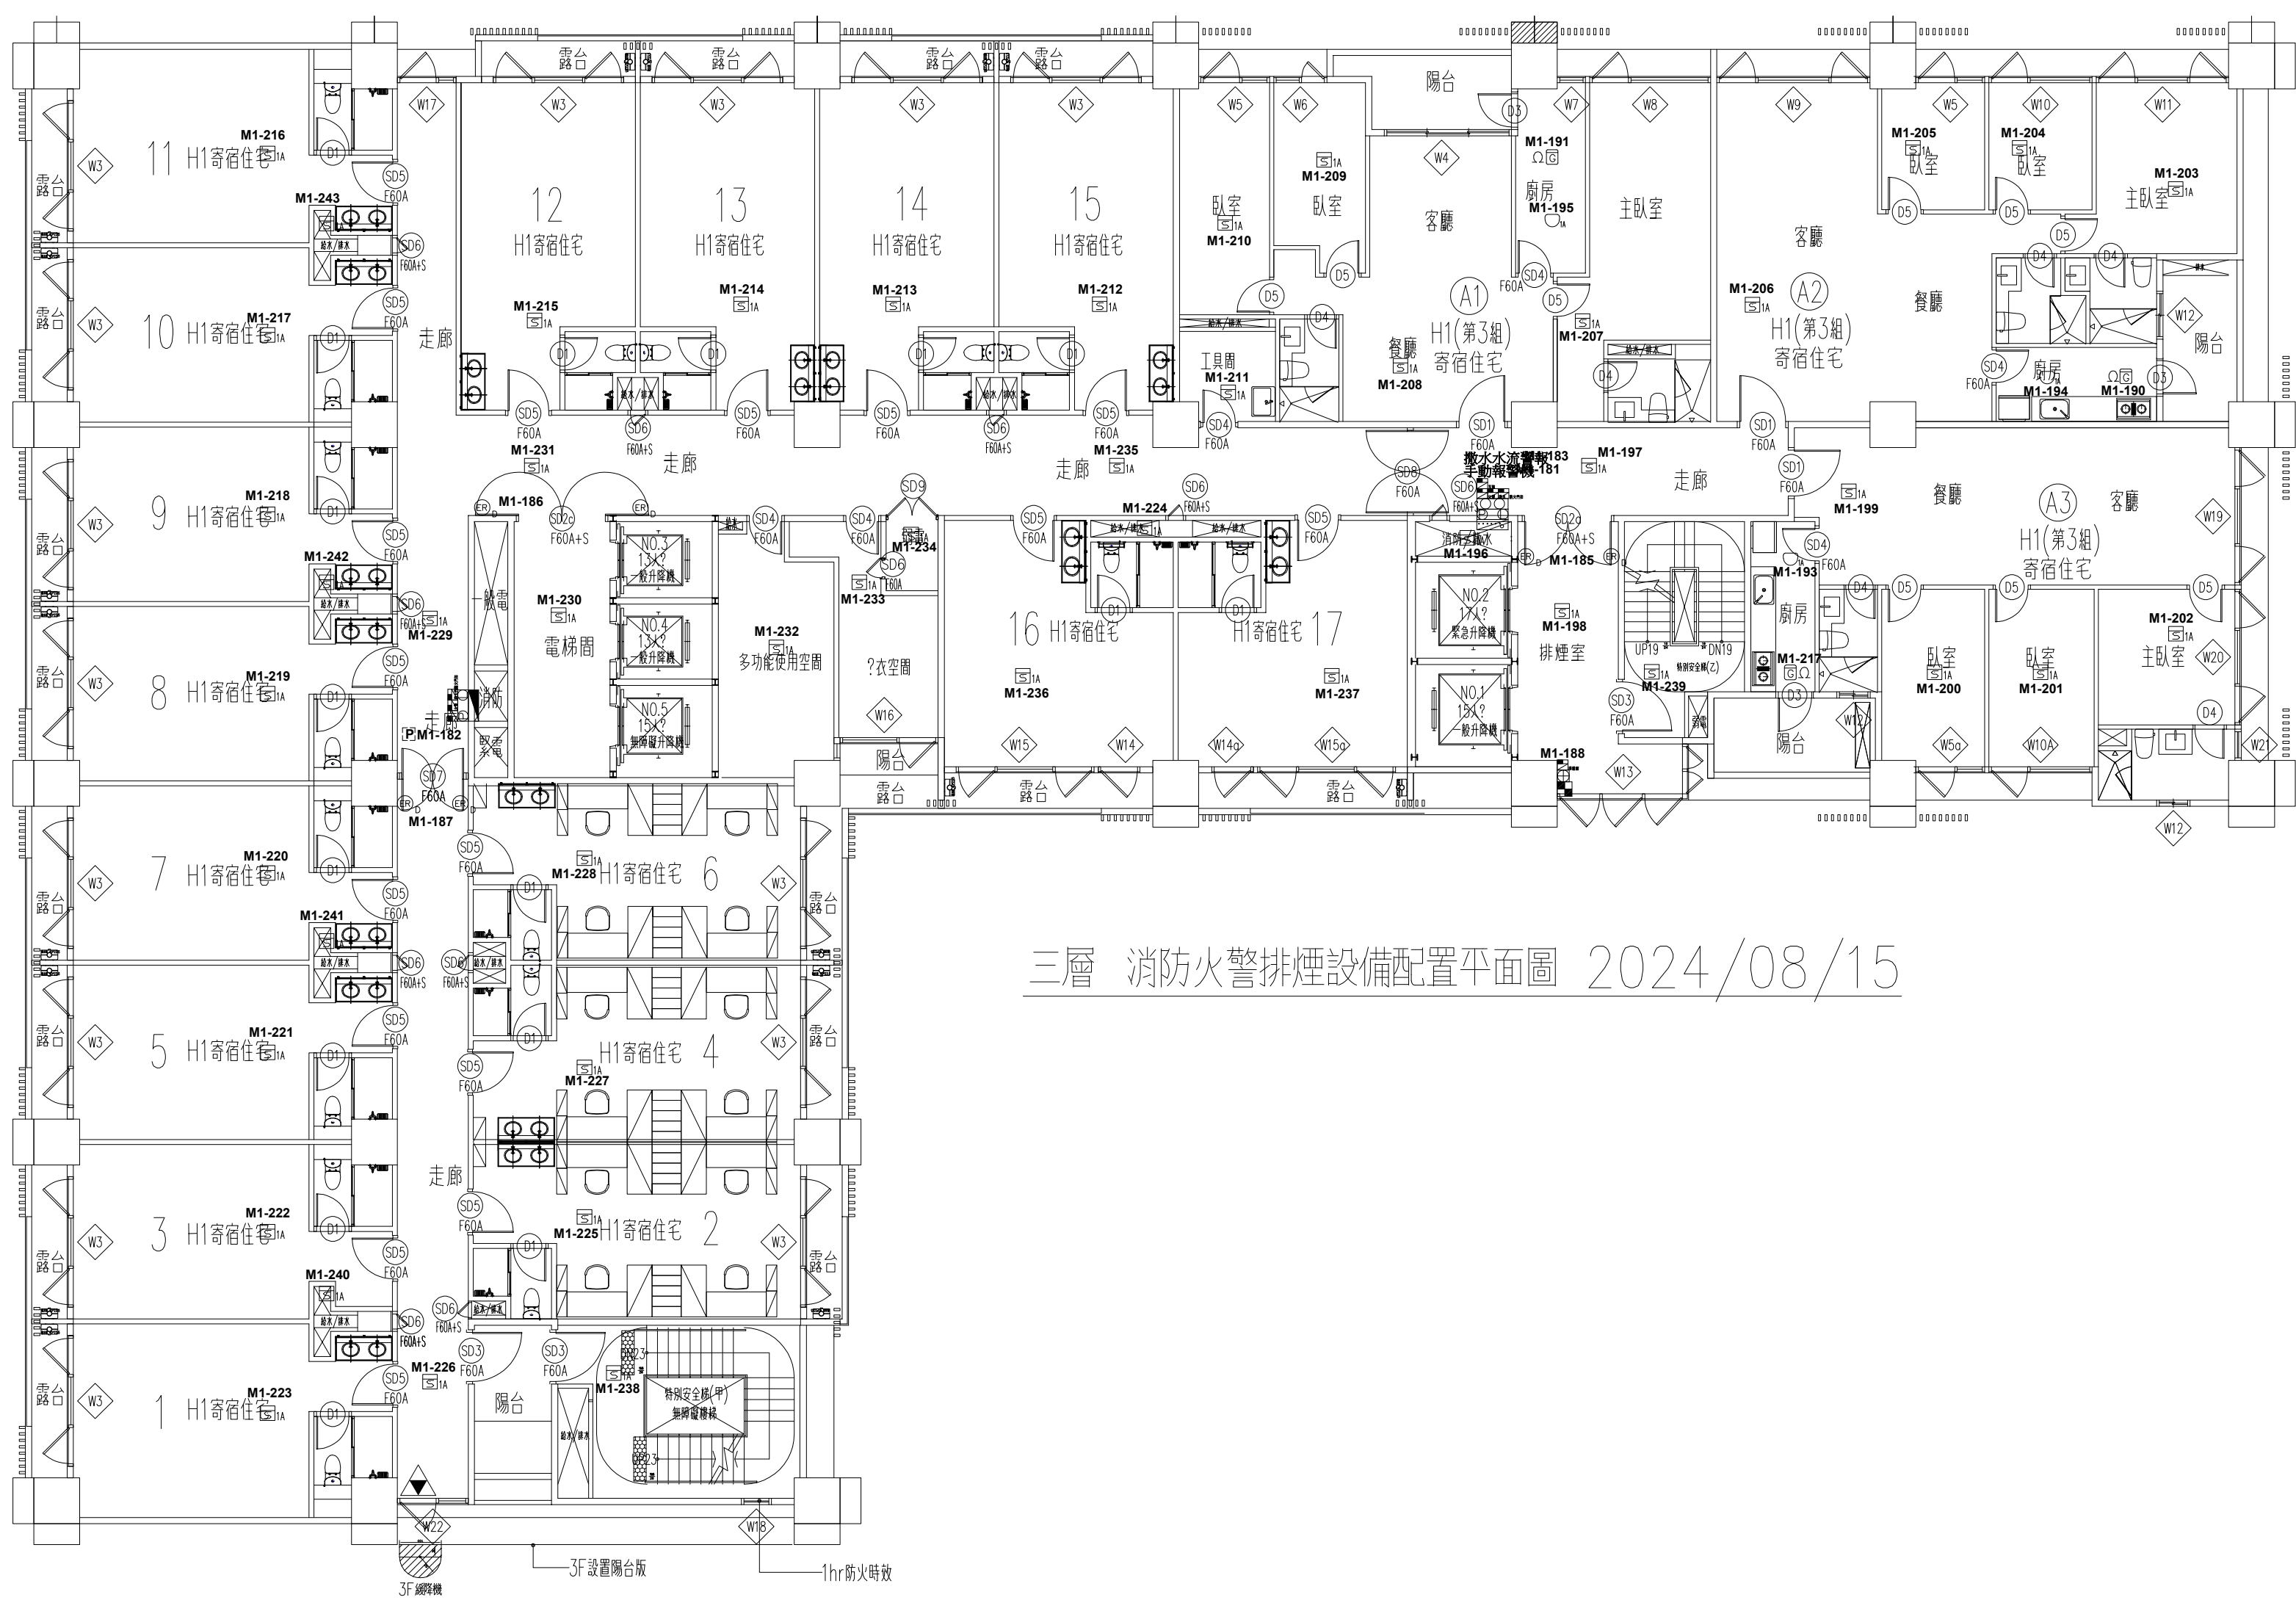

三層 消防火警排煙設備配置平面圖 2024/08/15

3F 鐵降機

3F 設置陽台板

1hr 防火時效