


# NODE:31

## 職務官舍2F

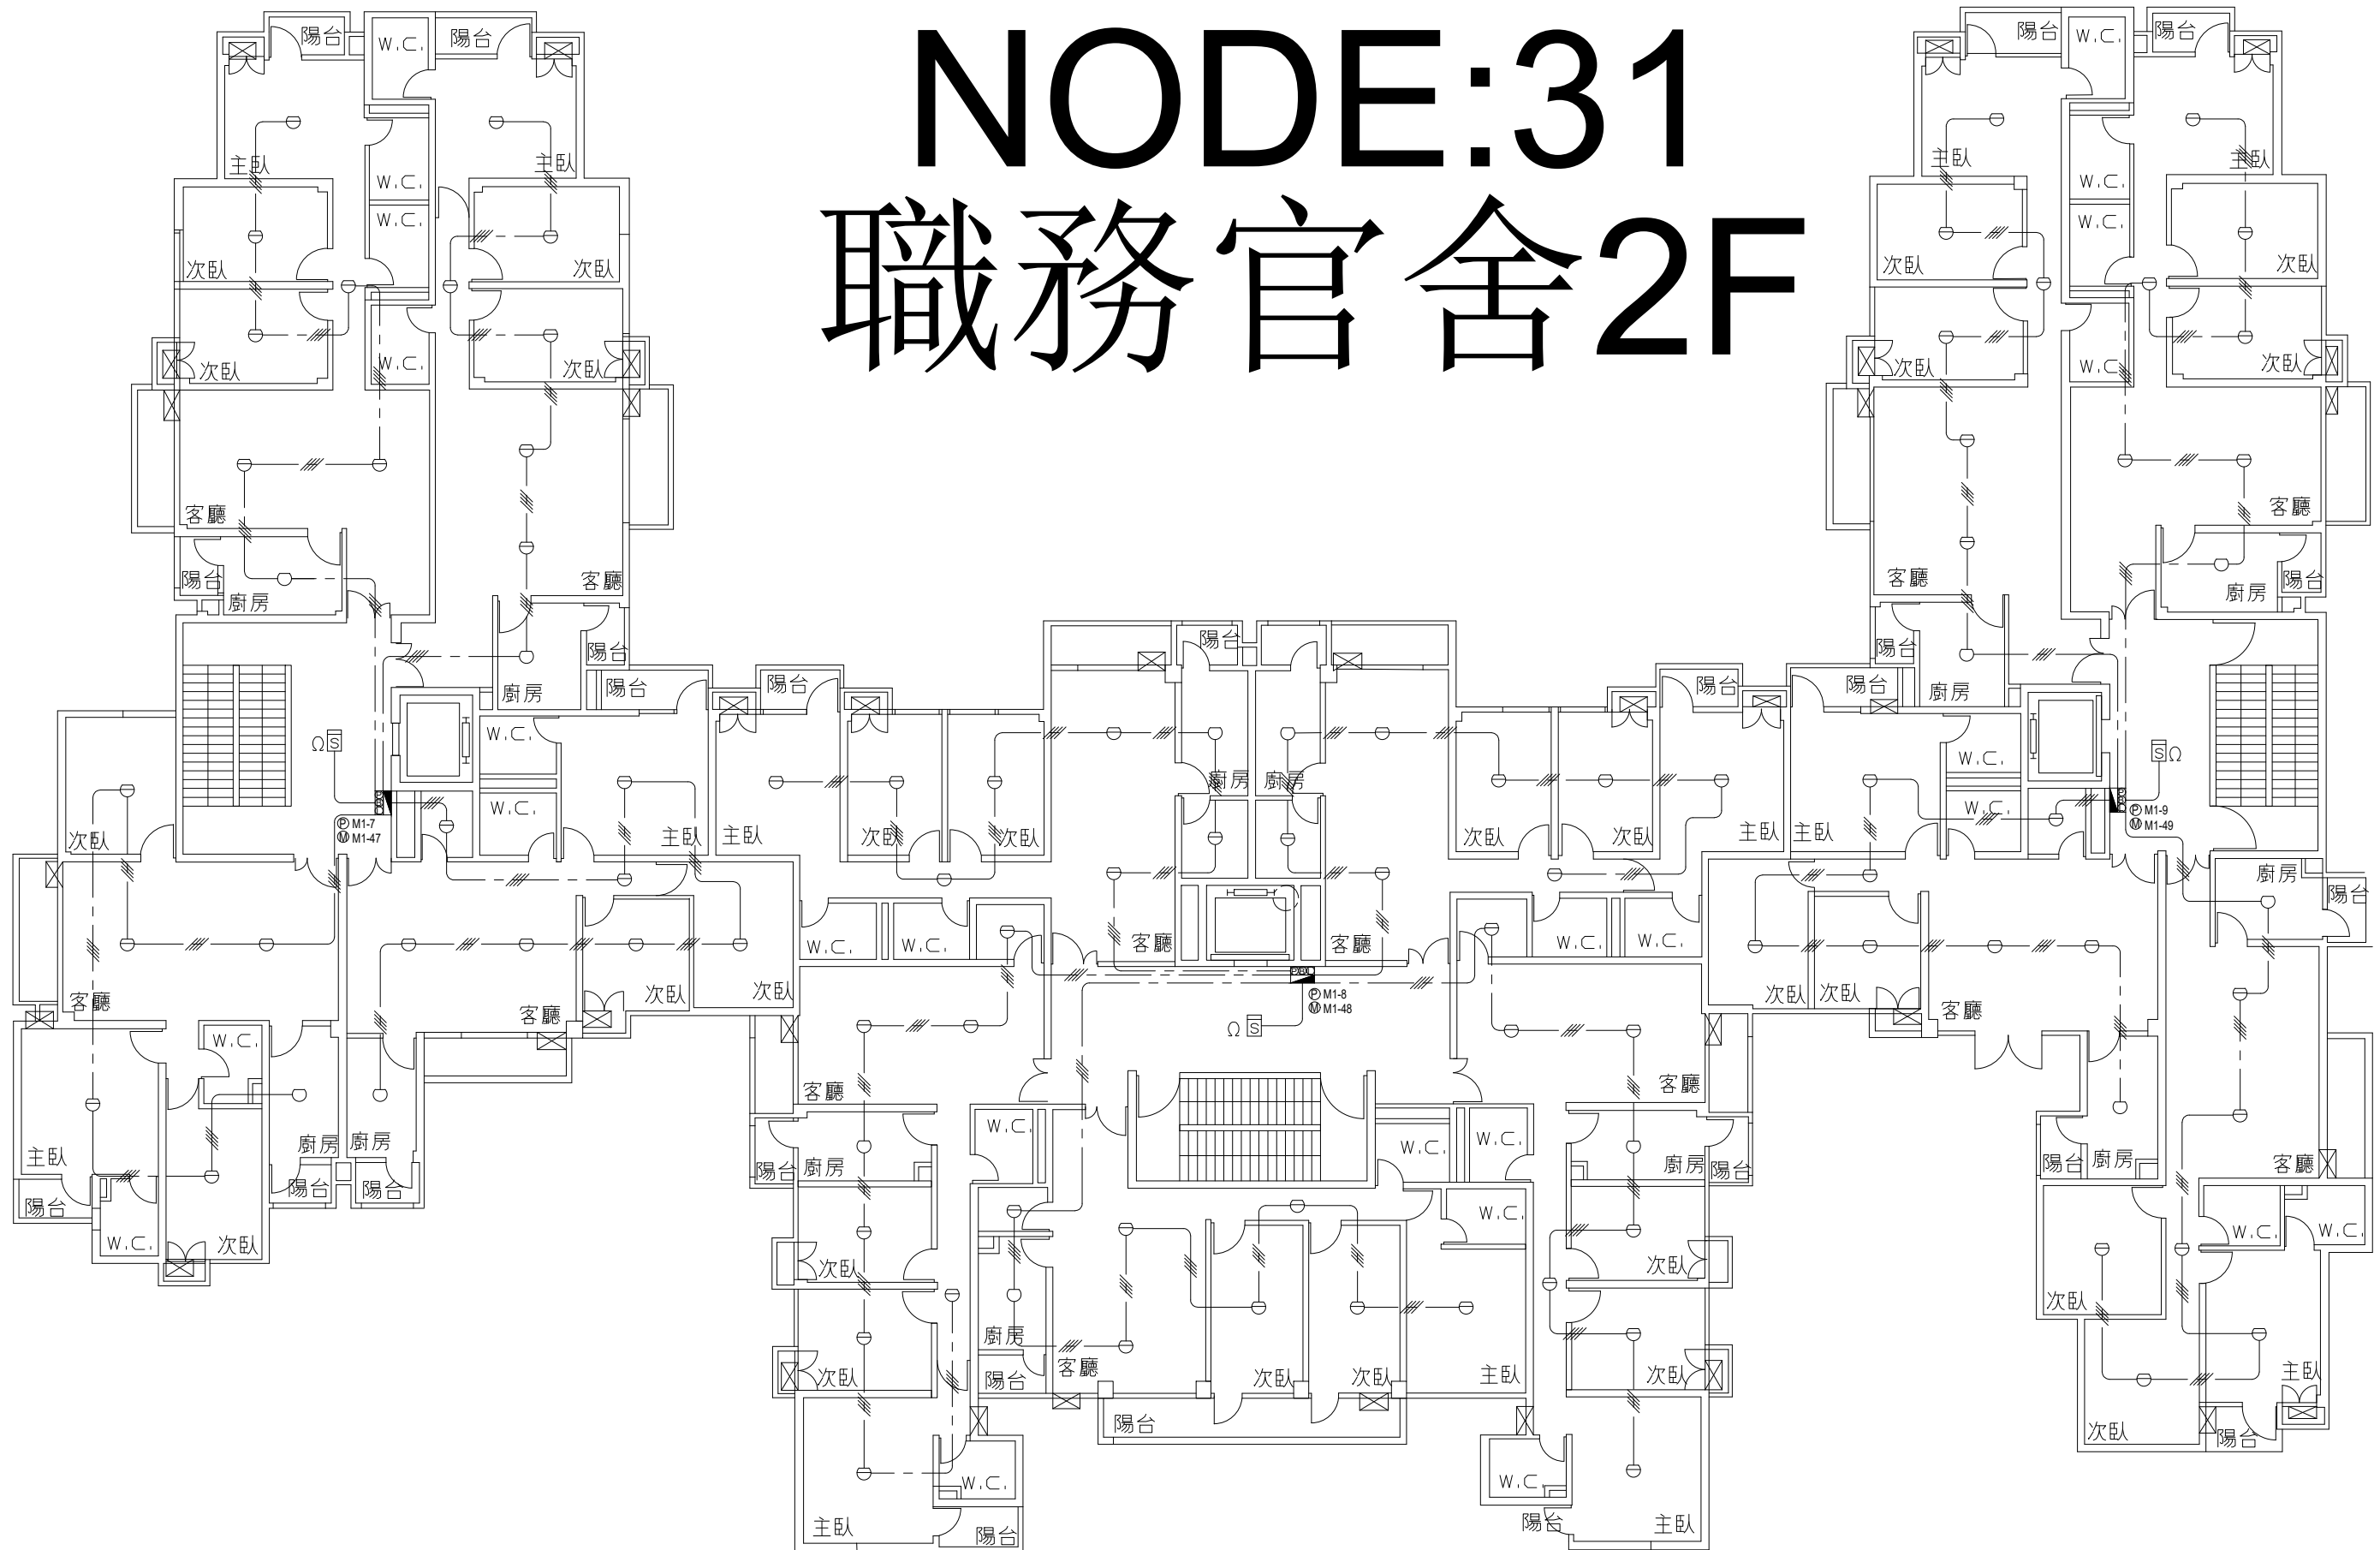

數量表

| 圖例 | 名稱    | 數量 |
|----|-------|----|
|    | 綜合消防栓 | 3  |
|    | 定溫探測器 | 13 |
|    | 偵煙探測器 | 3  |
|    | 差動探測器 | 84 |

| 圖例 | 名稱                  | 數量 |
|----|---------------------|----|
|    | 定址型探測報警中繼器<br>(綜合盤) | 3  |
|    | 定址型探測報警中繼器<br>(迴路)  | 3  |