


NODE:31

職務官舍3F

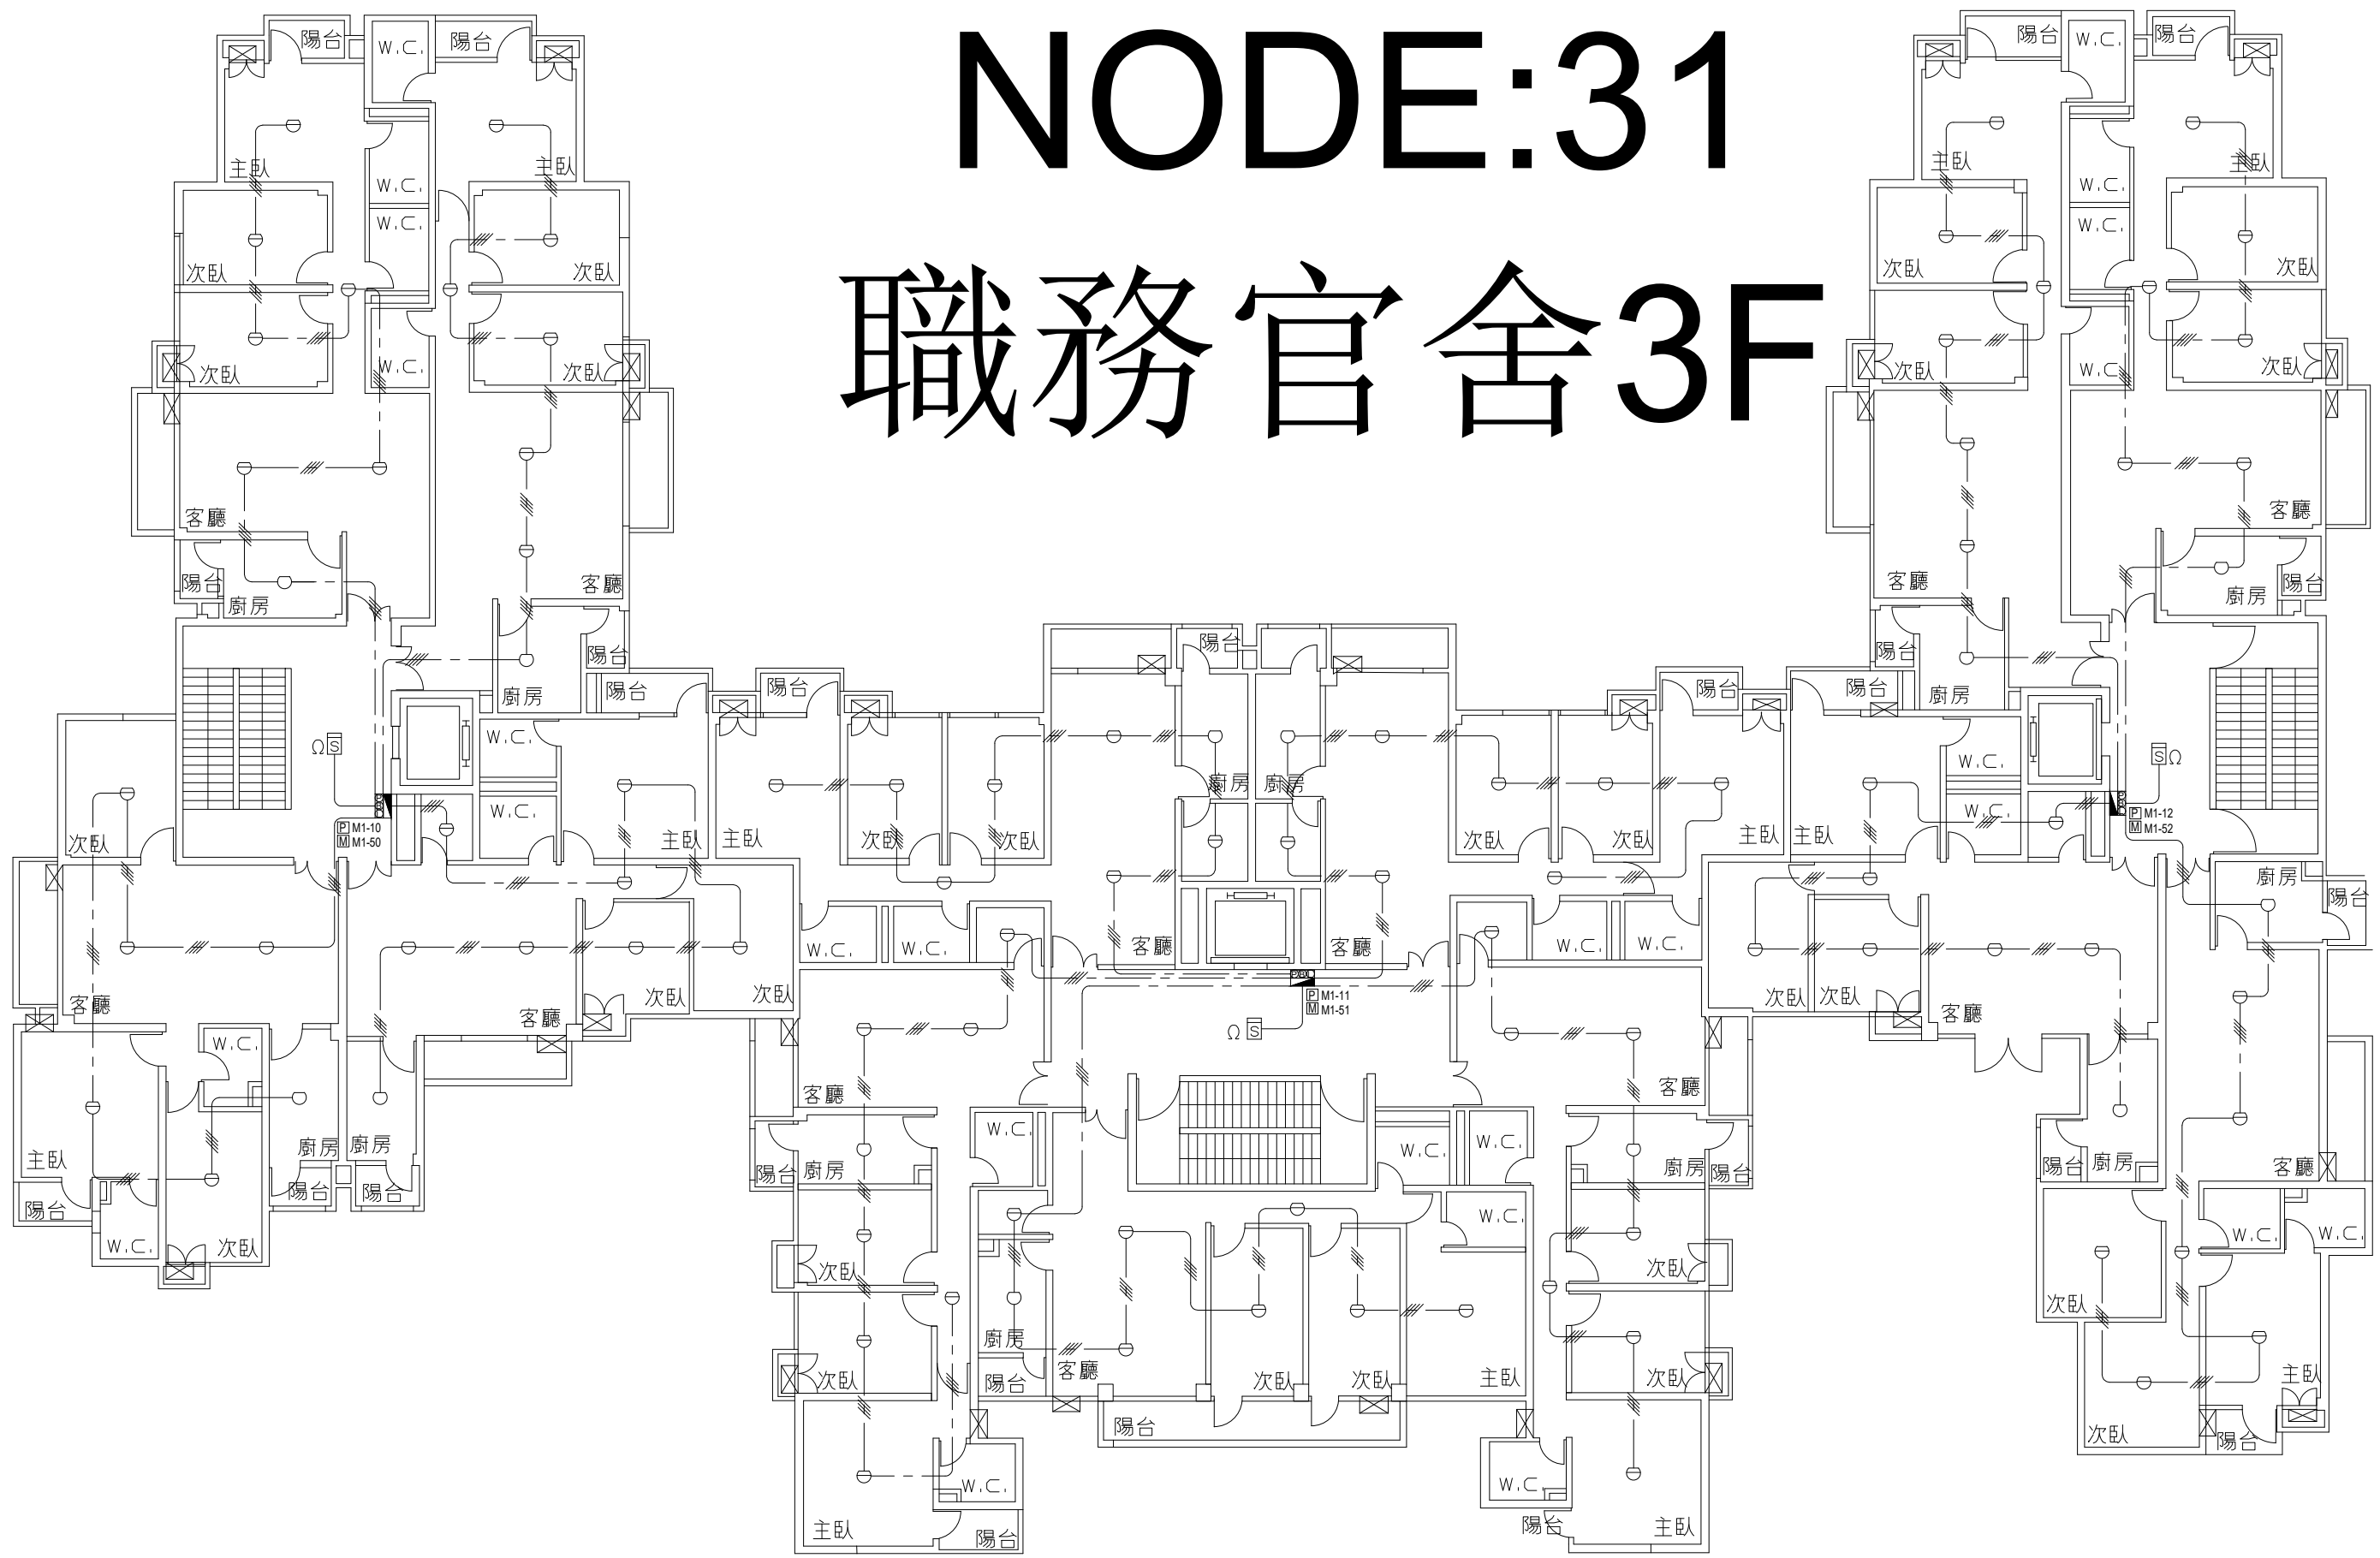

數量表

圖例	名稱	數量
	綜合消防栓	3
	定溫探測器	13
	偵煙探測器	3
	差動探測器	84

圖例	名稱	數量
	定址型模範監視中繼器 (綜合盤)	3
	定址型模範監視中繼器 (迴路)	3