


NODE:19

臨床1F

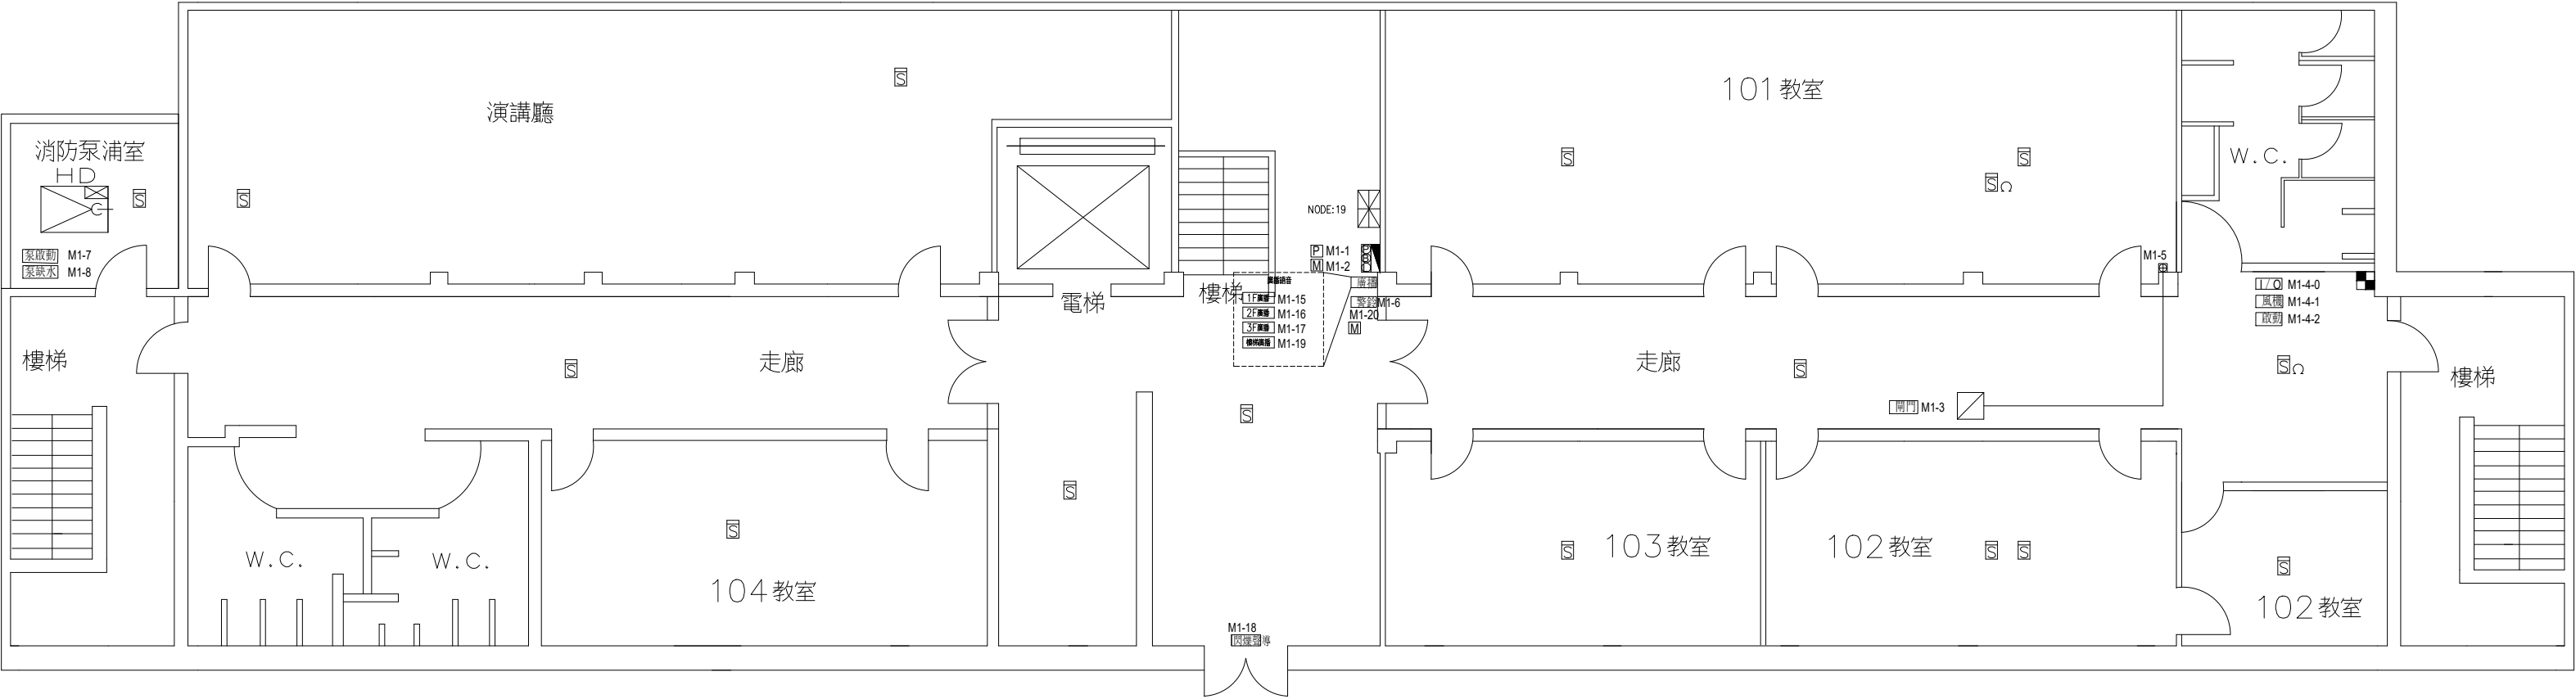

數 量 表

圖 例	名 稱	數 量
	綜合消防栓箱	1
	火警受信總機	1
	排煙控制盤	1
	排煙開門	1
	偵煙探測器	14

圖 例	名 稱	數 量
	定址型監視控制中繼器 (綜合盤)	1
	定址型監視控制中繼器 (迴路)	1
	定址型監視控制中繼器 (廣播主機)	4
	定址監視控制中繼器 (排煙控制盤)	1
	定址型控制中繼器 (排煙開門)	1

消防泵浦位於1F旁

圖 例	名 稱	數 量
	定址型控制中繼器 (泵啟動)	1
	定址型監視控制中繼器 (泵缺水狀態)	1