


# NODE:27

## 立體2F

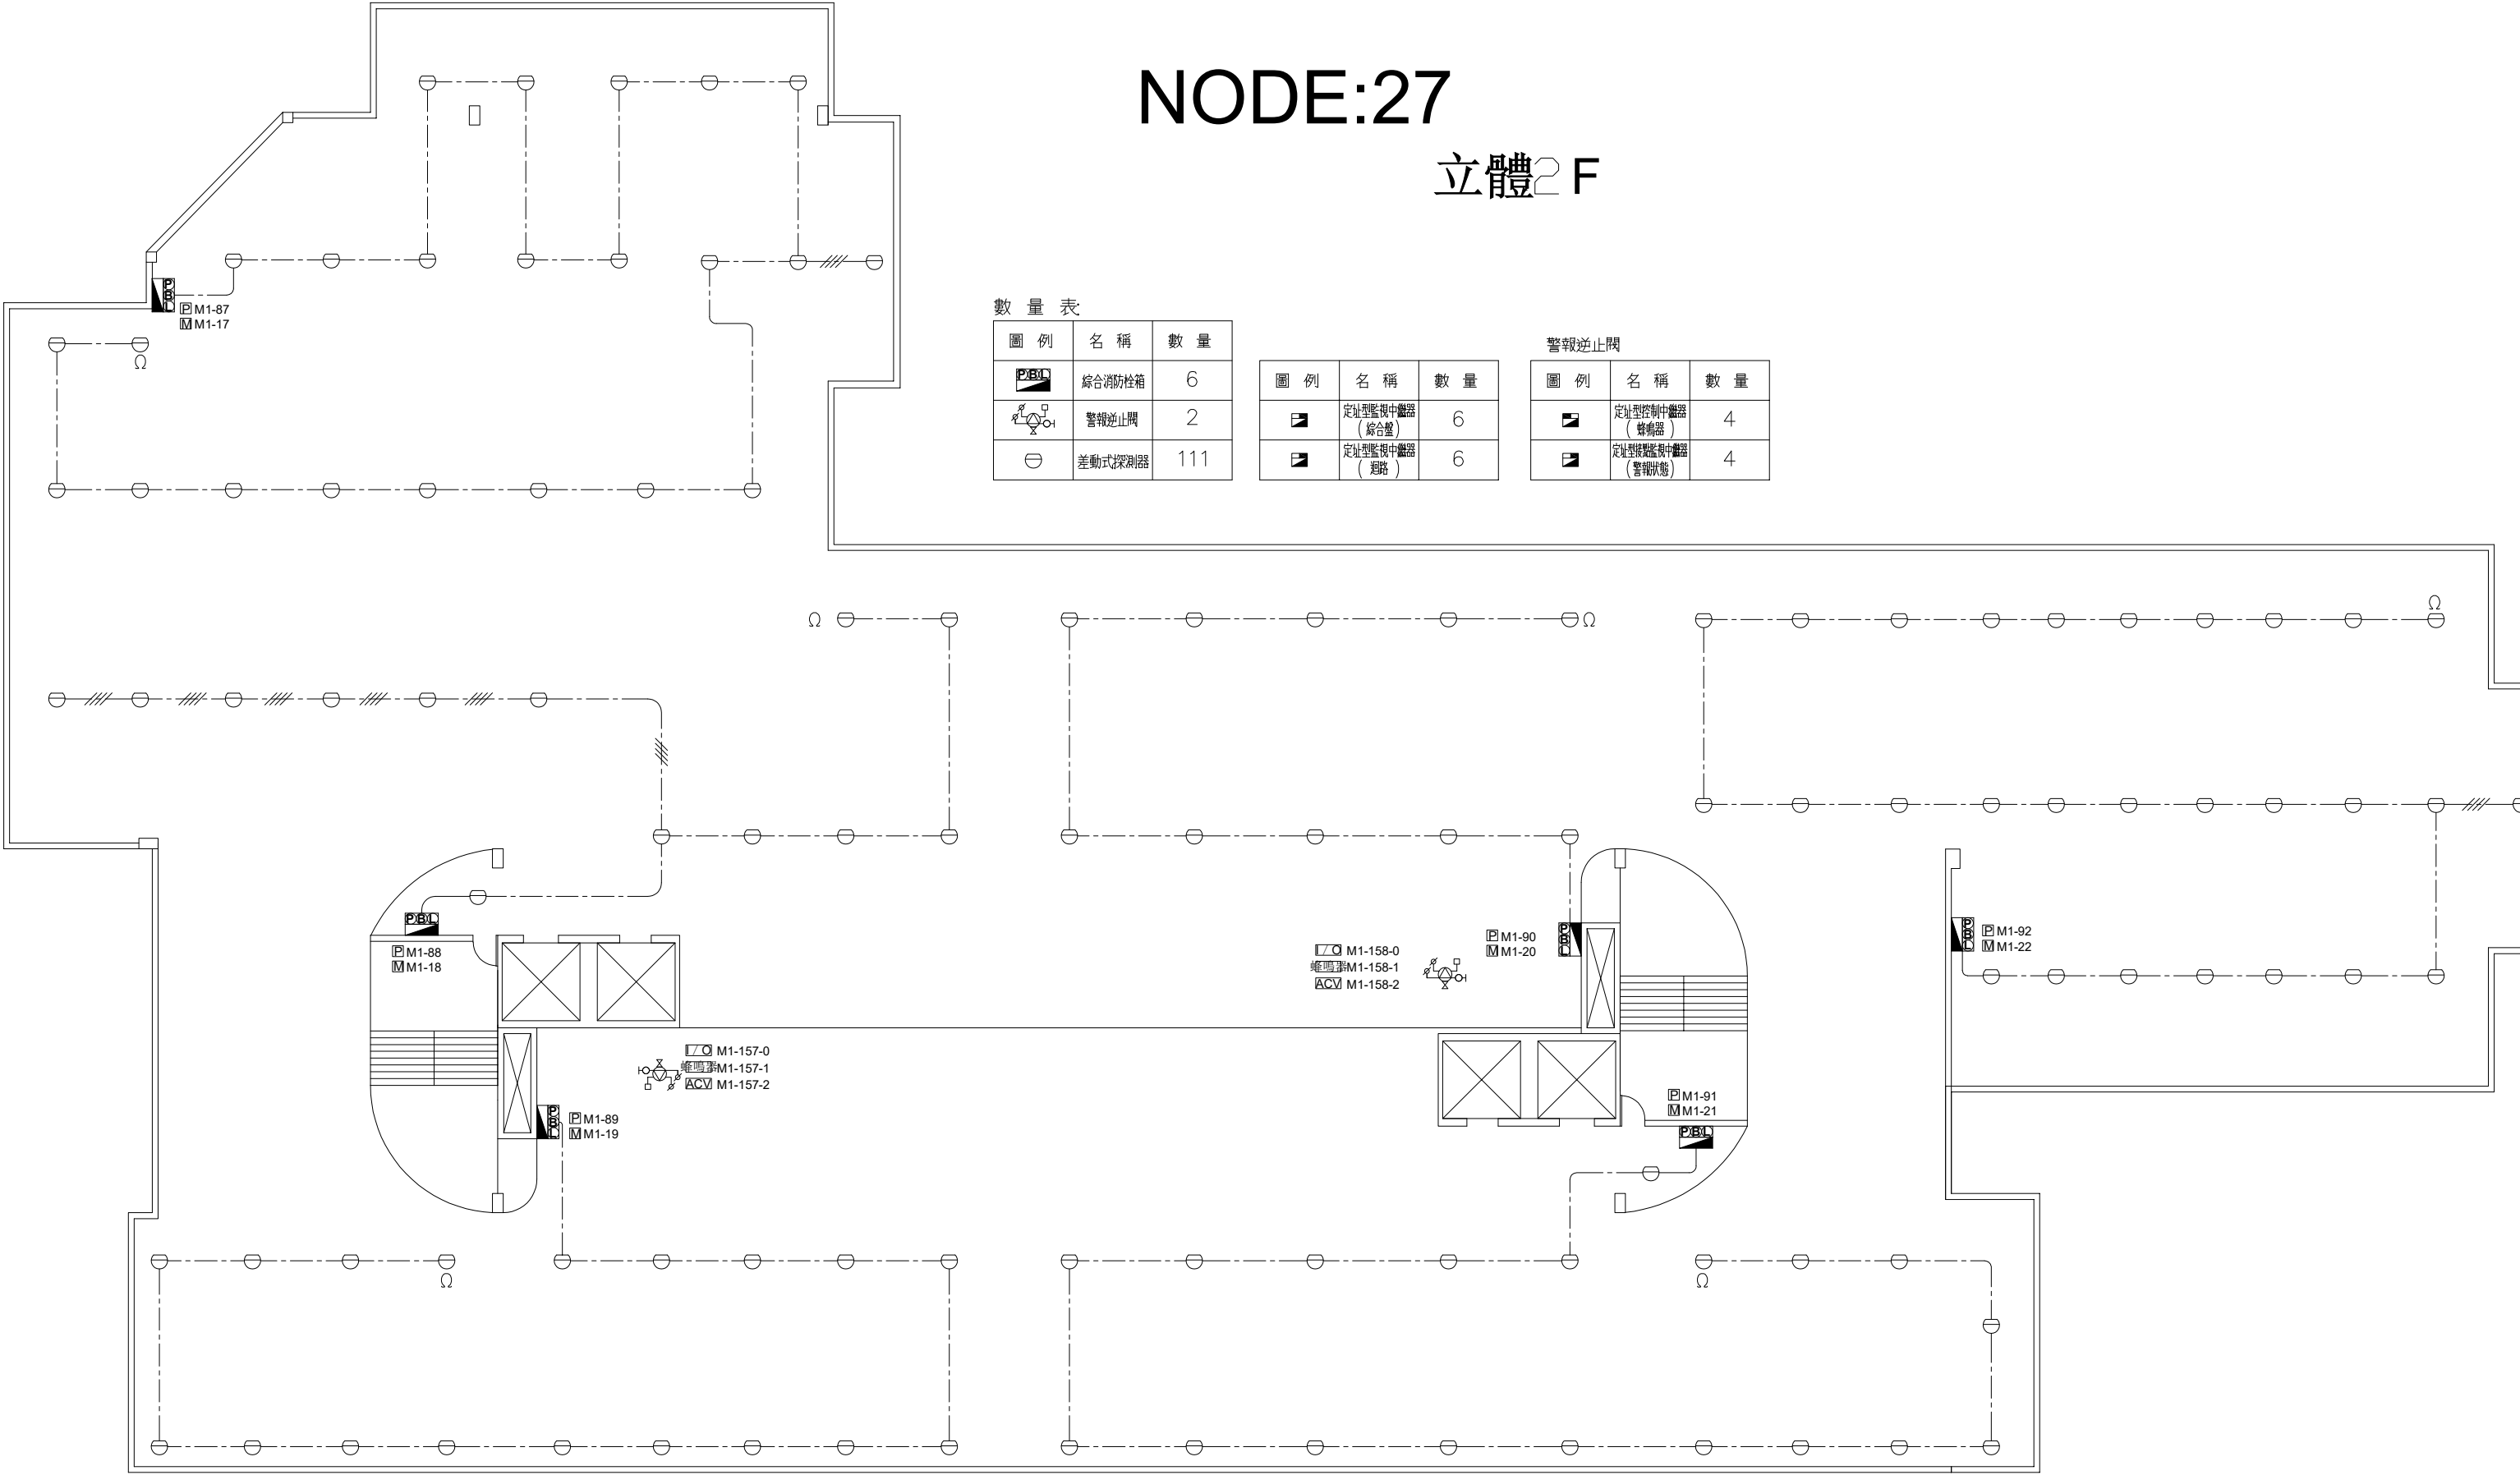

數 量 表

| 圖 例 | 名 稱    | 數 量 |
|-----|--------|-----|
|     | 綜合消防栓箱 | 6   |
|     | 警報逆止閥  | 2   |
|     | 差動式探測器 | 111 |

| 圖 例 | 名 稱               | 數 量 |
|-----|-------------------|-----|
|     | 定址型監視中繼器<br>(綜合盤) | 6   |
|     | 定址型監視中繼器<br>(迴路)  | 6   |

| 警報逆止閥 |                    |     |
|-------|--------------------|-----|
| 圖 例   | 名 稱                | 數 量 |
|       | 定址型控制中繼器<br>(綜合盤)  | 4   |
|       | 定址型監視中繼器<br>(警報狀態) | 4   |