


NODE:27

立體3F

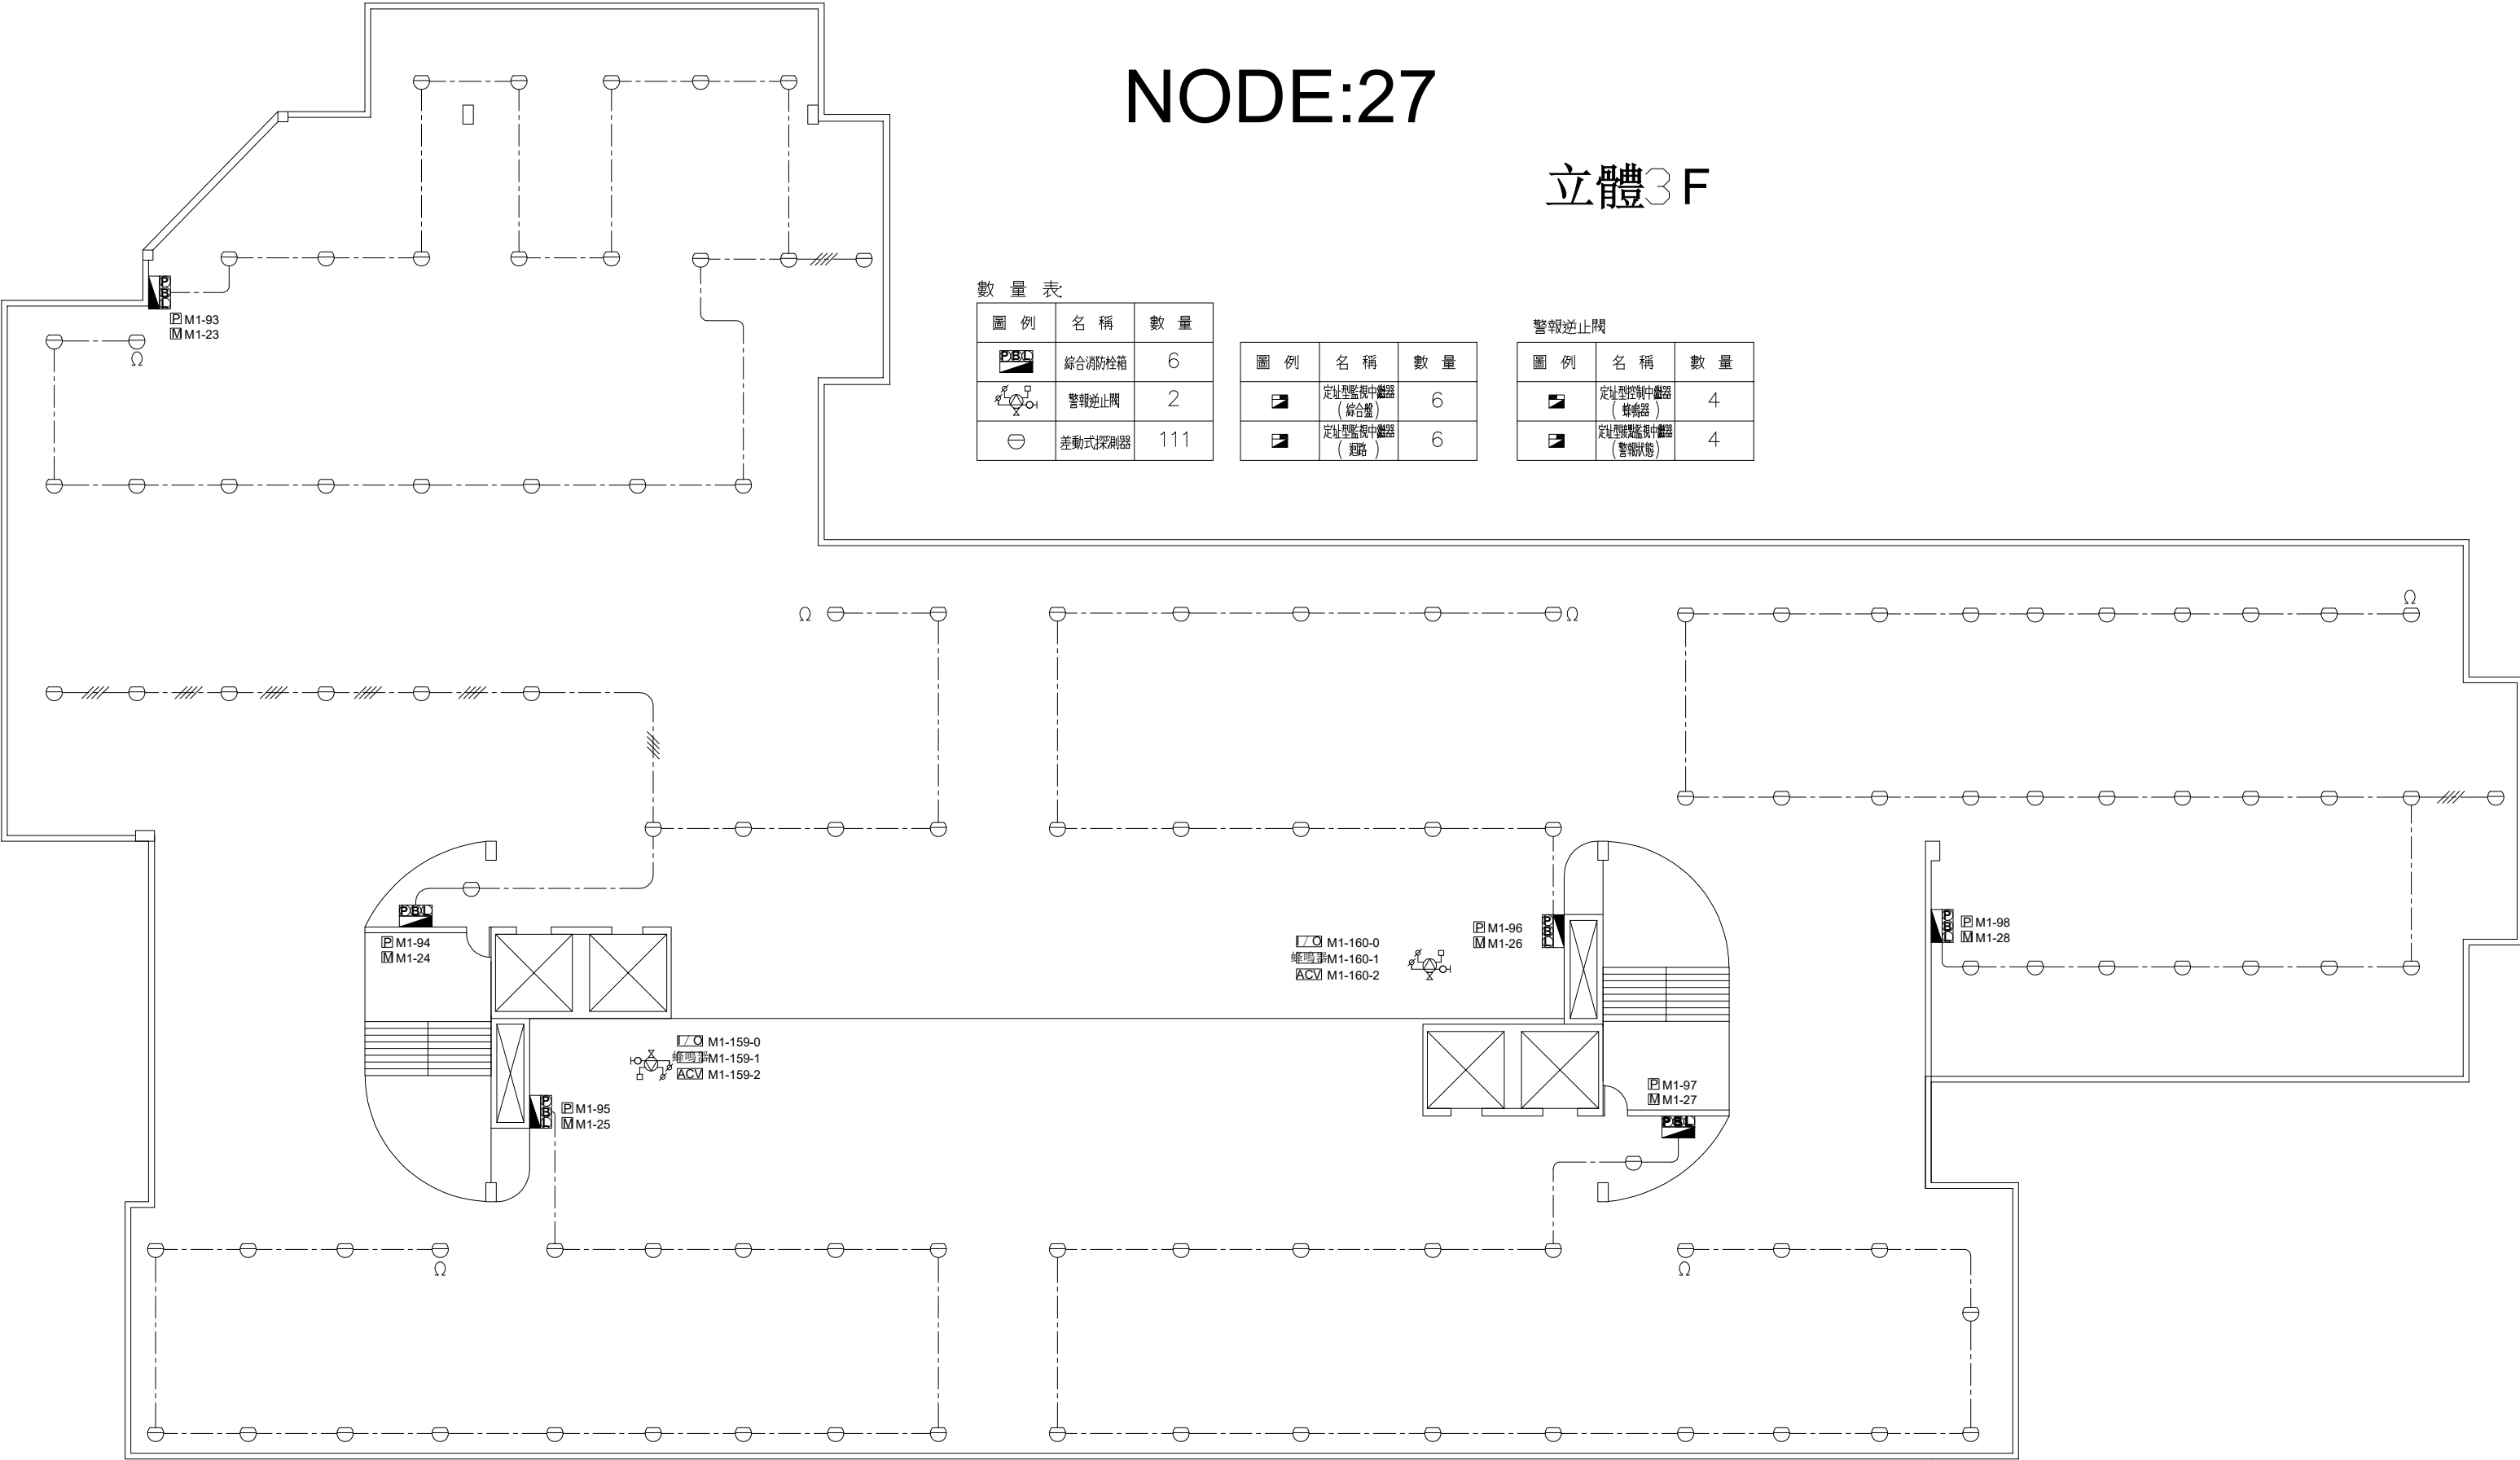

數量表

圖 例	名 稱	數 量
	綜合消防栓箱	6
	警報逆止閥	2
	差動式探測器	111

圖 例	名 稱	數 量
	定址型監視中繼器 (綜合盤)	6
	定址型監視中繼器 (迴路)	6

警報逆止閥

圖 例	名 稱	數 量
	定址型控制中繼器 (蜂鳴器)	4
	定址型監視中繼器 (警報狀態)	4