


NODE:27

立體 B2F

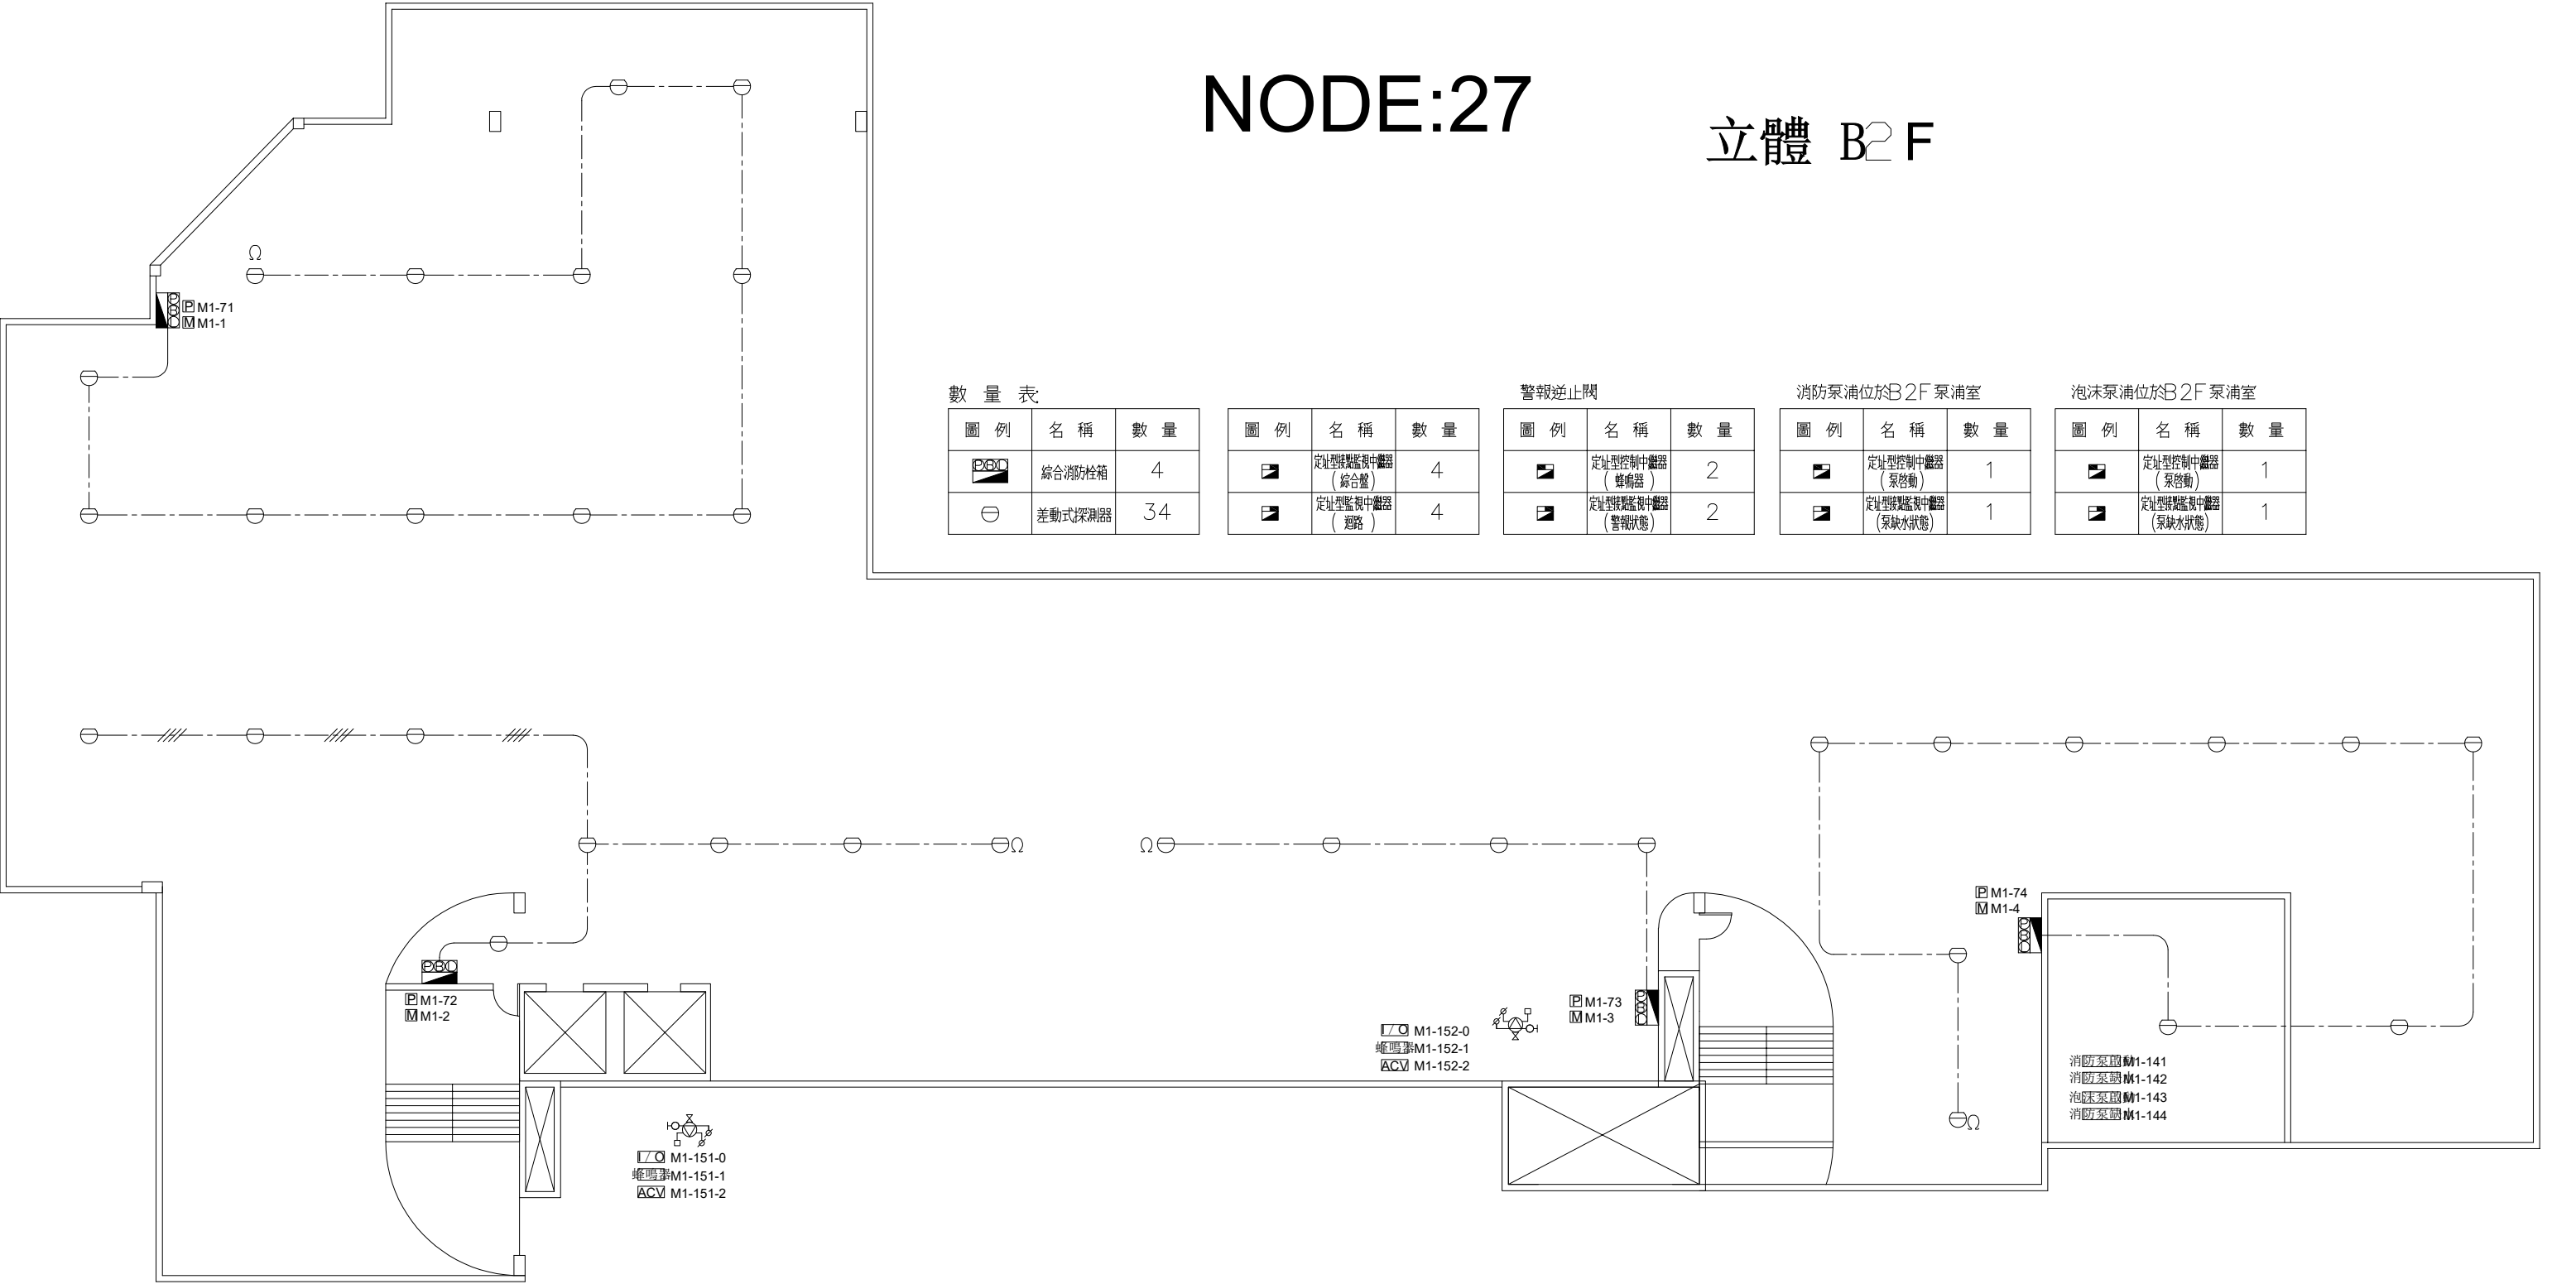

數 量 表

圖 例	名 稱	數 量
	綜合消防栓箱	4
	差動式探測器	34

圖 例	名 稱	數 量
	定址型探測監視中繼器 (綜合盤)	4
	定址型監視中繼器 (迴路)	4

警報逆止閥

圖 例	名 稱	數 量
	定址型控制中繼器 (蜂鳴器)	2
	定址型探測監視中繼器 (警報狀態)	2

消防泵浦位於B 2F 泵浦室

圖 例	名 稱	數 量
	定址型控制中繼器 (泵啟動)	1
	定址型探測監視中繼器 (泵缺水狀態)	1

泡沫泵浦位於B 2F 泵浦室

圖 例	名 稱	數 量
	定址型控制中繼器 (泵啟動)	1
	定址型探測監視中繼器 (泵缺水狀態)	1